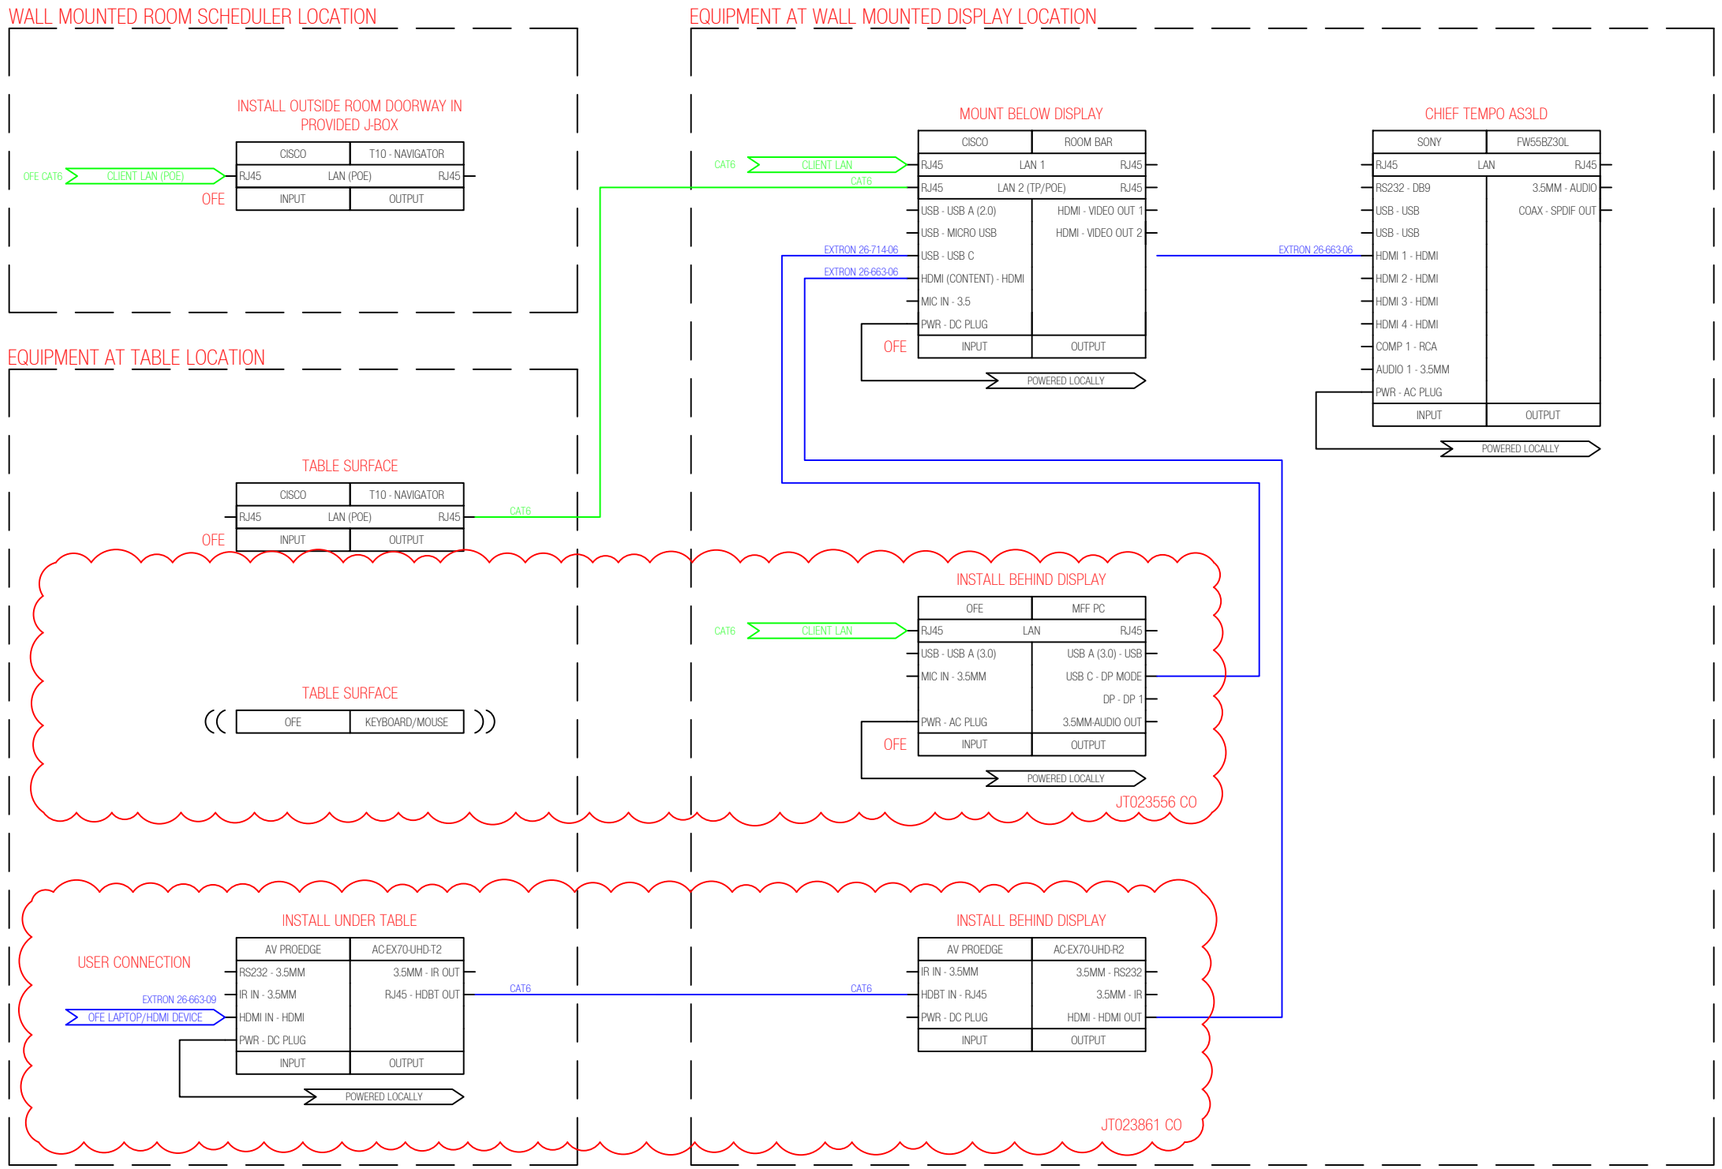

LEAD TECHNICIAN (PRINT): _____

NETWORK REQUIREMENTS			POWER REQUIREMENTS		
QTY	DEVICE	LOCATION	QTY	CIRCUIT/SIZE	LOCATION
1	ROOMBAR	DISPLAY LOCATION	1	15A QUAD	DISPLAY LOCATION
1	ROOM SCHEDULER	OUTSIDE ROOM	-	-	-
1	OFE PC	WALL (BEHIND DISPLAY)	-	-	-
-	-	-	-	-	-
-	-	-	-	-	-
-	-	-	-	-	-
-	-	-	-	-	-
-	-	-	-	-	-
-	-	-	-	-	-
-	-	-	-	-	-

CLIENT NAME: LOCKTON DUNNING

REV:	DATE:	DRAWN BY:
0	03/05/2026	AFS
-	-	-

TAURUS technologies
1420 LAKESIDE PARKWAY, SUITE 100, FLOWER MOUND, TX 75028
WWW.TAURUSTECHINC.COM 1-888-410-5747

ROOM NAME: VICTORY COMMONS - 14TH FLOOR - HUDDLE ROOM 14.033

SITE ADDRESS: 2601 VICTORY AVE, DALLAS, TX 75219

PROJECT NO: JT022715, JT023560, JT023785, JT023822, JT023861 & JT023995

SHEET SIZE:	SCALE:	SHEET NO:
11 X 17	1 : 1	TA-701

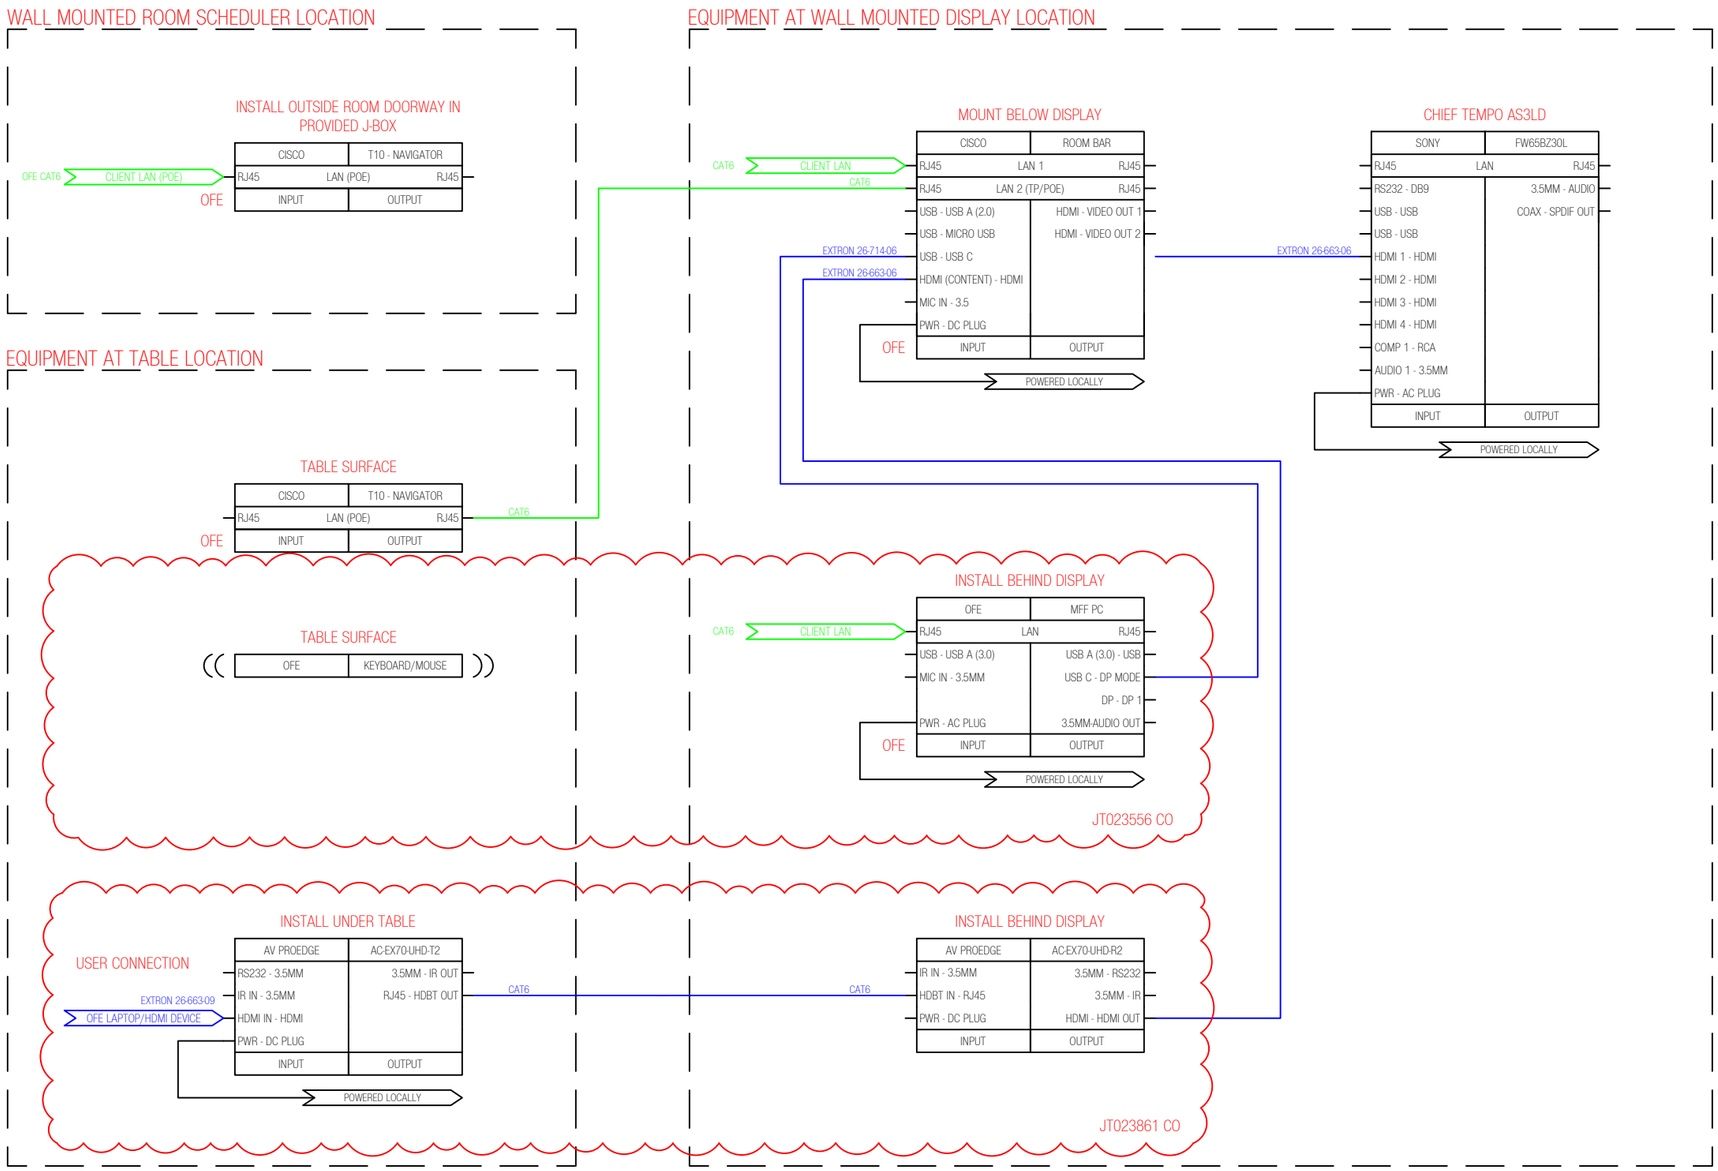

LEAD TECHNICIAN (PRINT): _____

NETWORK REQUIREMENTS			POWER REQUIREMENTS		
QTY	DEVICE	LOCATION	QTY	CIRCUIT/SIZE	LOCATION
1	ROOMBAR	DISPLAY LOCATION	1	15A QUAD	DISPLAY LOCATION
1	ROOM SCHEDULER	OUTSIDE ROOM	-	-	-
1	OFE PC	WALL (BEHIND DISPLAY)	-	-	-
-	-	-	-	-	-
-	-	-	-	-	-
-	-	-	-	-	-
-	-	-	-	-	-
-	-	-	-	-	-
-	-	-	-	-	-
-	-	-	-	-	-

CLIENT NAME: LOCKTON DUNNING

REV:	DATE:	DRAWN BY:
0	03/05/2026	AFS
-	-	-

TAURUS technologies
1420 LAKESIDE PARKWAY, SUITE 100, FLOWER MOUND, TX 75028
WWW.TAURUSTECHINC.COM 1-888-410-5747

ROOM NAME: VICTORY COMMONS - 14TH FLOOR - HUDDLE ROOM 14.044

SITE ADDRESS: 2601 VICTORY AVE, DALLAS, TX 75219

PROJECT NO: JT022715, JT023560, JT023785, JT023822, JT023861 & JT023995

SHEET SIZE:	SCALE:	SHEET NO:
11 X 17	1 : 1	TA-702

LEAD TECH NOTE: THIS ROOM HAS BEEN REMOVED FROM OUR SCOPE, ALL EQUIPMENT HAS BEEN RETURNED TO THE MANUFACTURE OR CLIENT IF OFE (CO JT023995)

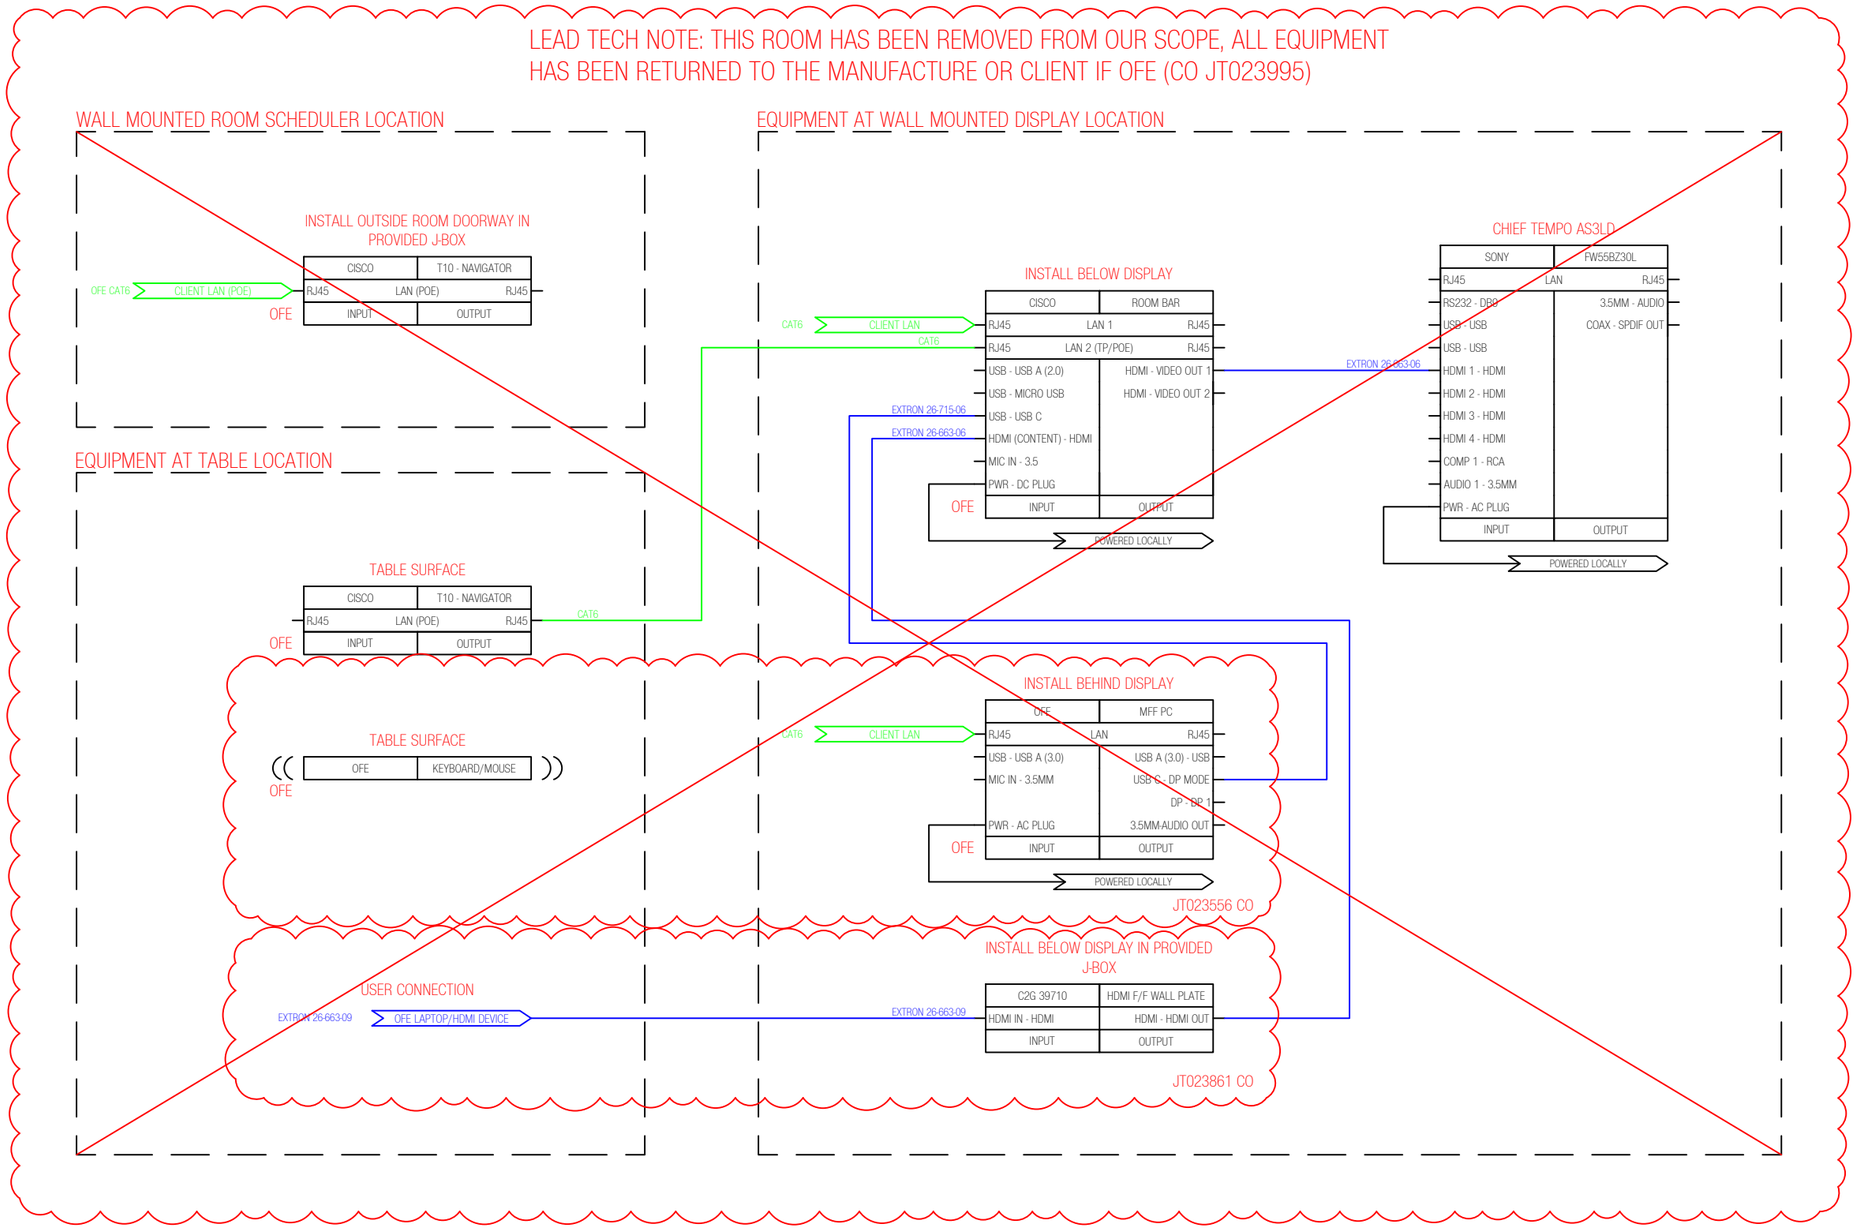

LEAD TECHNICIAN (PRINT): _____

NETWORK REQUIREMENTS			POWER REQUIREMENTS		
QTY	DEVICE	LOCATION	QTY	CIRCUIT/SIZE	LOCATION
1	ROOMBAR	DISPLAY LOCATION	1	15A QUAD	DISPLAY LOCATION
1	ROOM SCHEDULER	OUTSIDE ROOM	-	-	-
1	OFE PC	WALL (BEHIND DISPLAY)	-	-	-
-	-	-	-	-	-
-	-	-	-	-	-
-	-	-	-	-	-
-	-	-	-	-	-
-	-	-	-	-	-
-	-	-	-	-	-
-	-	-	-	-	-

CLIENT NAME: LOCKTON DUNNING

REV:	DATE:	DRAWN BY:
0	03/05/2026	AFS
-	-	-

TAURUS technologies
1420 LAKESIDE PARKWAY, SUITE 100, FLOWER MOUND, TX 75028
WWW.TAURUSTECHINC.COM 1-888-410-5747

ROOM NAME: VICTORY COMMONS - 14TH FLOOR - HUDDLE ROOM 14.096

SITE ADDRESS: 2601 VICTORY AVE, DALLAS, TX 75219

PROJECT NO: JT022715, JT023560, JT023785, JT023822, JT023861 & JT023995

SHEET SIZE:	SCALE:	SHEET NO:
11 X 17	1 : 1	TA-703

LEAD TECH NOTE: THIS ROOM HAS BEEN REMOVED FROM OUR SCOPE, ALL EQUIPMENT HAS BEEN RETURNED TO THE MANUFACTURE OR CLIENT IF OFE (CO JT023995)

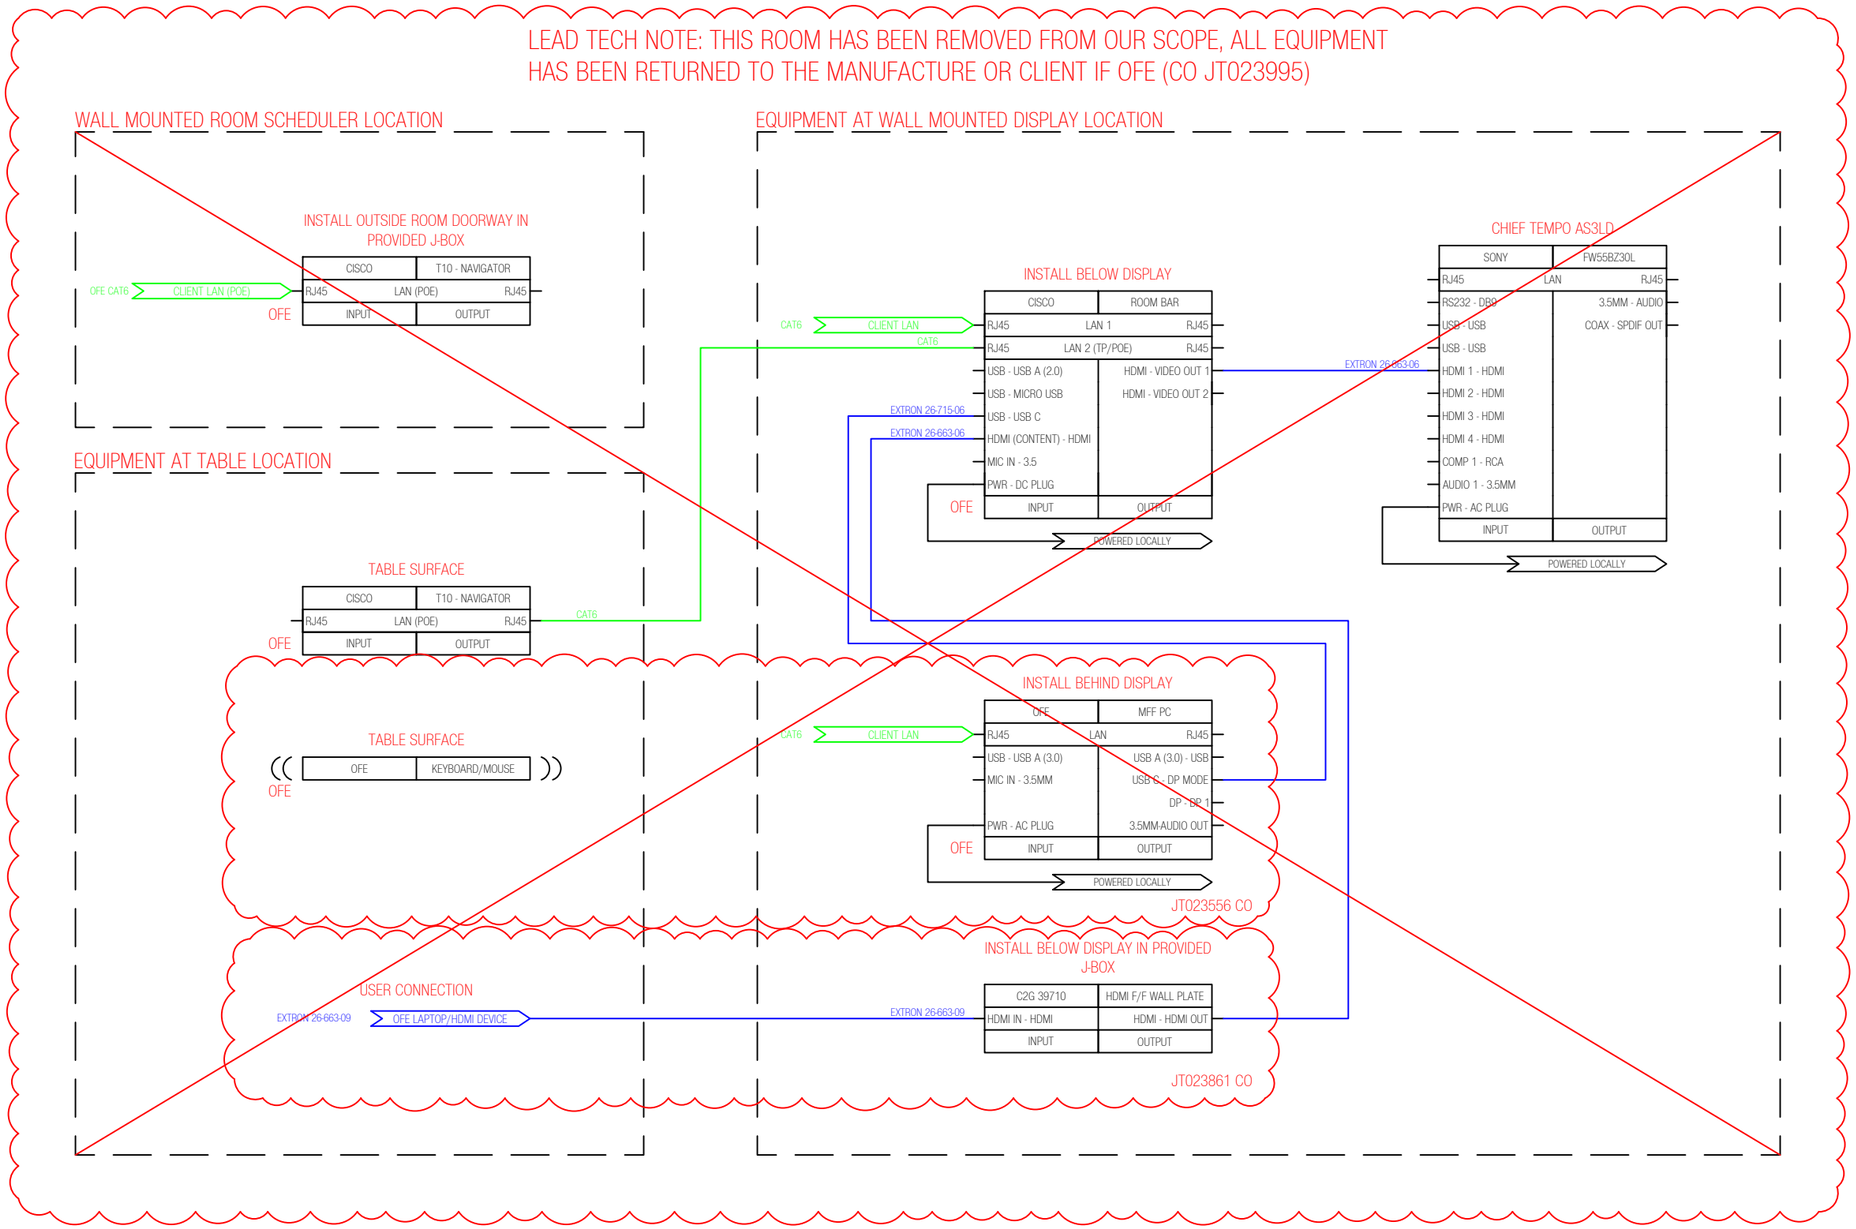

LEAD TECHNICIAN (PRINT): _____

NETWORK REQUIREMENTS			POWER REQUIREMENTS		
QTY	DEVICE	LOCATION	QTY	CIRCUIT/SIZE	LOCATION
1	ROOMBAR	DISPLAY LOCATION	1	15A QUAD	DISPLAY LOCATION
1	ROOM SCHEDULER	OUTSIDE ROOM	-	-	-
1	OFE PC	WALL (BEHIND DISPLAY)	-	-	-
-	-	-	-	-	-
-	-	-	-	-	-
-	-	-	-	-	-
-	-	-	-	-	-
-	-	-	-	-	-
-	-	-	-	-	-
-	-	-	-	-	-

CLIENT NAME: LOCKTON DUNNING

REV:	DATE:	DRAWN BY:
0	03/05/2026	AFS
-	-	-

TAURUS technologies
1420 LAKESIDE PARKWAY, SUITE 100, FLOWER MOUND, TX 75028
WWW.TAURUSTECHINC.COM 1-888-410-5747

ROOM NAME: VICTORY COMMONS - 14TH FLOOR - HUDDLE ROOM 14.097

SITE ADDRESS: 2601 VICTORY AVE, DALLAS, TX 75219

PROJECT NO: JT022715, JT023560, JT023785, JT023822, JT023861 & JT023995

SHEET SIZE:	SCALE:	SHEET NO:
11 X 17	1 : 1	TA-704

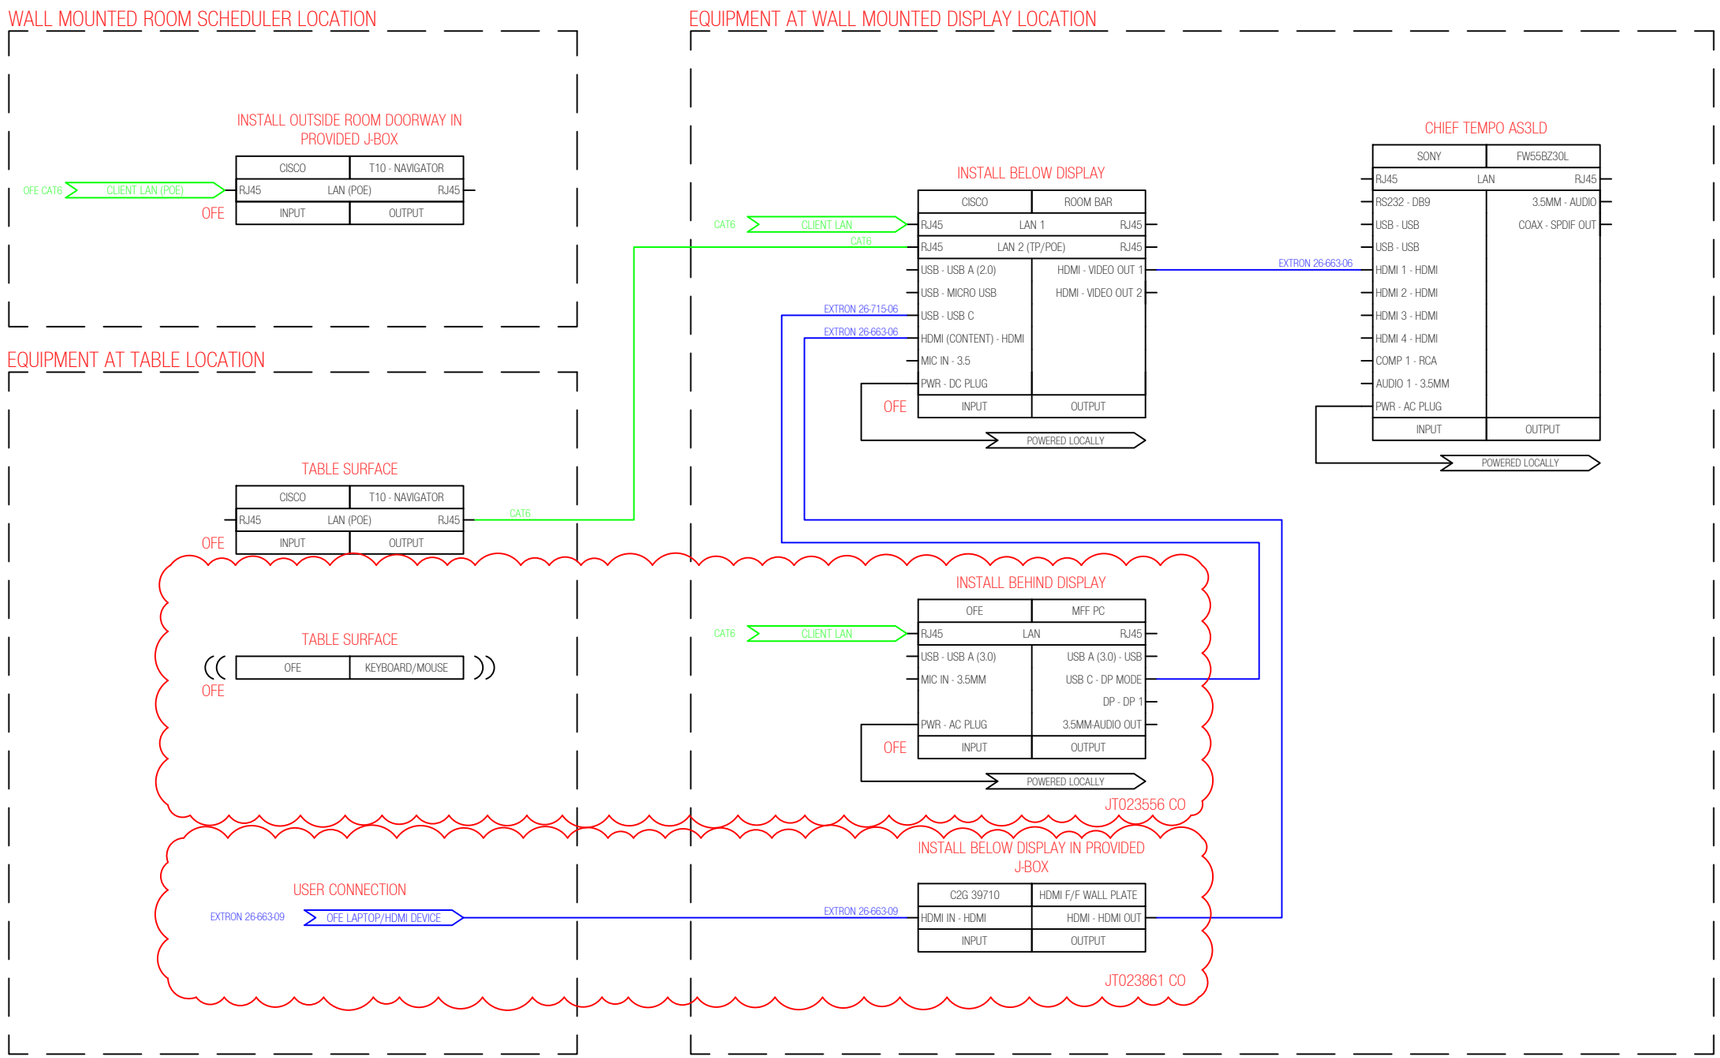

LEAD TECHNICIAN (PRINT): _____

NETWORK REQUIREMENTS			POWER REQUIREMENTS		
QTY	DEVICE	LOCATION	QTY	CIRCUIT/SIZE	LOCATION
1	ROOMBAR	DISPLAY LOCATION	1	15A QUAD	DISPLAY LOCATION
1	ROOM SCHEDULER	OUTSIDE ROOM	-	-	-
1	OFE PC	WALL (BEHIND DISPLAY)	-	-	-
-	-	-	-	-	-
-	-	-	-	-	-
-	-	-	-	-	-
-	-	-	-	-	-
-	-	-	-	-	-
-	-	-	-	-	-
-	-	-	-	-	-
-	-	-	-	-	-

CLIENT NAME: LOCKTON DUNNING

REV:	DATE:	DRAWN BY:
0	03/05/2026	AFS
-	-	-

TAURUS technologies
1420 LAKESIDE PARKWAY, SUITE 100, FLOWER MOUND, TX 75028
WWW.TAURUSTECHINC.COM 1-888-410-5747

ROOM NAME: VICTORY COMMONS - 14TH FLOOR - HUDDLE ROOM 14.105

SITE ADDRESS: 2601 VICTORY AVE, DALLAS, TX 75219

PROJECT NO: JT022715, JT023560, JT023785, JT023822, JT023861 & JT023995

SHEET SIZE:	SCALE:	SHEET NO:
11 X 17	1 : 1	TA-705

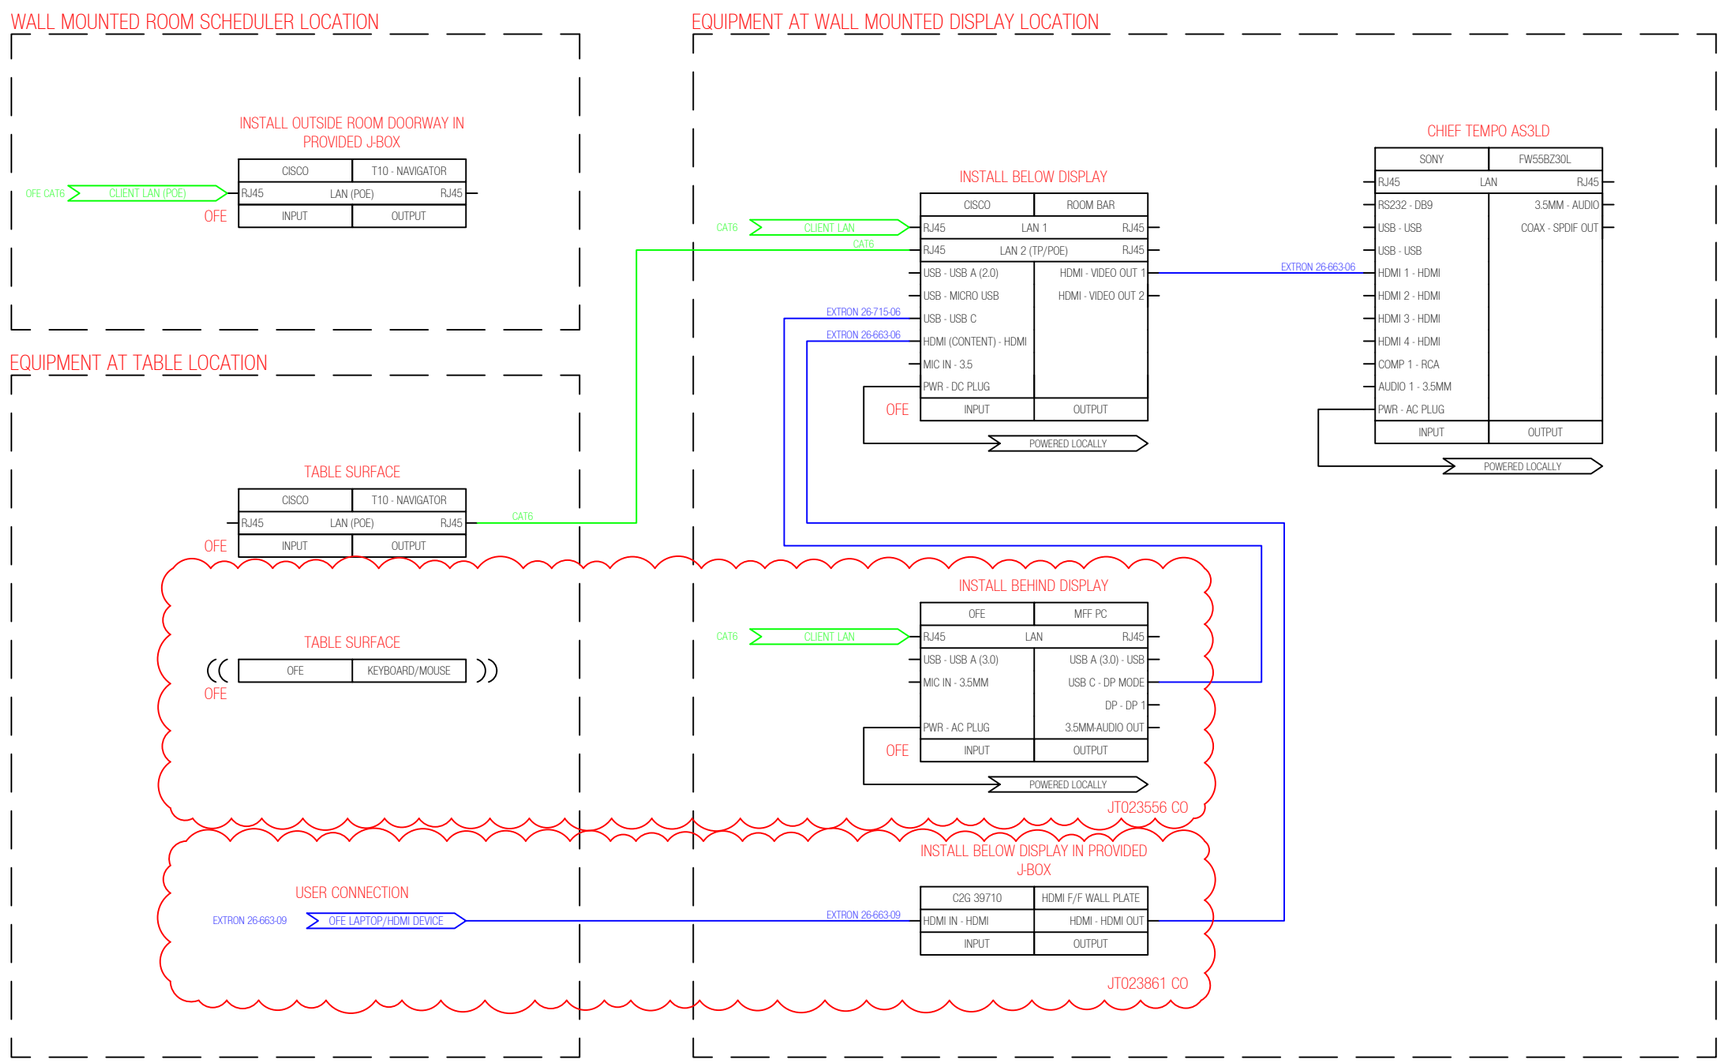

LEAD TECHNICIAN (PRINT): _____

NETWORK REQUIREMENTS			POWER REQUIREMENTS		
QTY	DEVICE	LOCATION	QTY	CIRCUIT/SIZE	LOCATION
1	ROOMBAR	DISPLAY LOCATION	1	15A QUAD	DISPLAY LOCATION
1	ROOM SCHEDULER	OUTSIDE ROOM	-	-	-
1	OFE PC	WALL (BEHIND DISPLAY)	-	-	-
-	-	-	-	-	-
-	-	-	-	-	-
-	-	-	-	-	-
-	-	-	-	-	-
-	-	-	-	-	-
-	-	-	-	-	-
-	-	-	-	-	-

CLIENT NAME: LOCKTON DUNNING

REV:	DATE:	DRAWN BY:
0	03/05/2026	AFS
-	-	-

TAURUS technologies
1420 LAKESIDE PARKWAY, SUITE 100, FLOWER MOUND, TX 75028
WWW.TAURUSTECHINC.COM 1-888-410-5747

ROOM NAME: VICTORY COMMONS - 14TH FLOOR - HUDDLE ROOM 14.106

SITE ADDRESS: 2601 VICTORY AVE, DALLAS, TX 75219

PROJECT NO: JT022715, JT023560, JT023785, JT023822, JT023861 & JT023995

SHEET SIZE:	SCALE:	SHEET NO:
11 X 17	1 : 1	TA-706

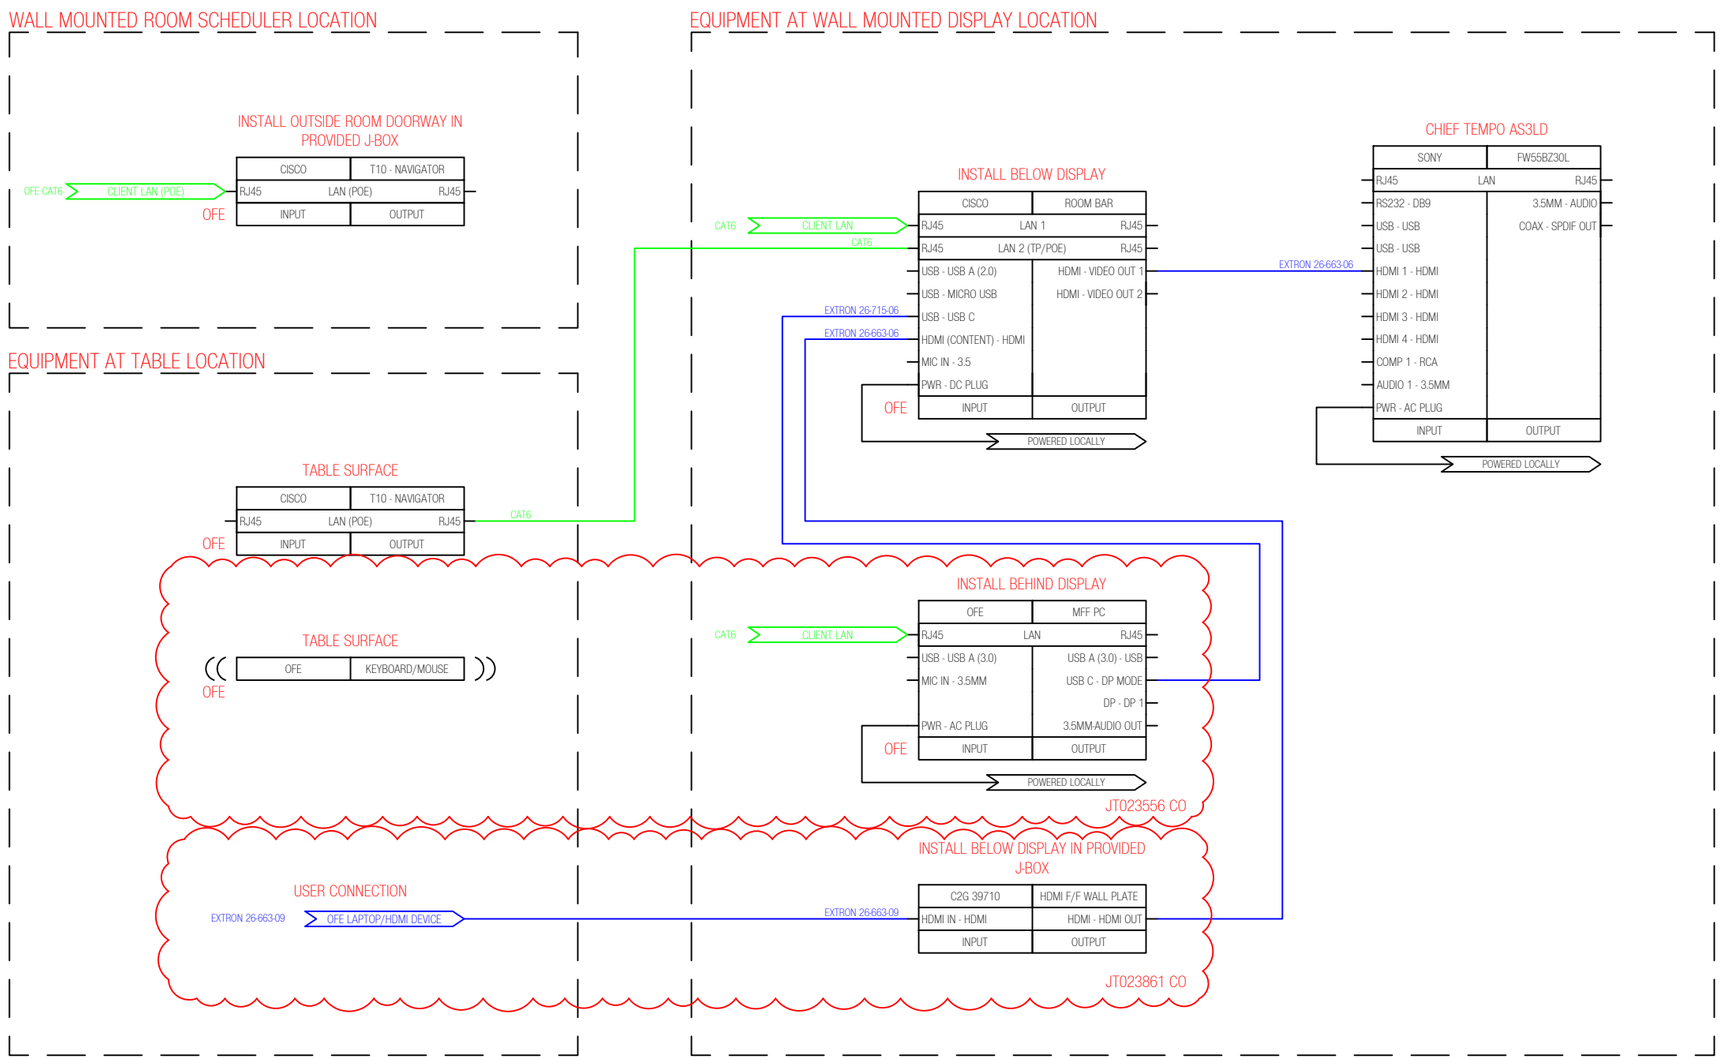

LEAD TECHNICIAN (PRINT): _____

NETWORK REQUIREMENTS			POWER REQUIREMENTS		
QTY	DEVICE	LOCATION	QTY	CIRCUIT/SIZE	LOCATION
1	ROOMBAR	DISPLAY LOCATION	1	15A QUAD	DISPLAY LOCATION
1	ROOM SCHEDULER	OUTSIDE ROOM	-	-	-
1	OFE PC	WALL (BEHIND DISPLAY)	-	-	-
-	-	-	-	-	-
-	-	-	-	-	-
-	-	-	-	-	-
-	-	-	-	-	-
-	-	-	-	-	-
-	-	-	-	-	-
-	-	-	-	-	-

CLIENT NAME: LOCKTON DUNNING

REV:	DATE:	DRAWN BY:
0	03/05/2026	AFS
-	-	-

TAURUS technologies
1420 LAKESIDE PARKWAY, SUITE 100, FLOWER MOUND, TX 75028
WWW.TAURUSTECHINC.COM 1-888-410-5747

ROOM NAME: VICTORY COMMONS - 15TH FLOOR - HUDDLE ROOM 15.033

SITE ADDRESS: 2601 VICTORY AVE, DALLAS, TX 75219

PROJECT NO: JT022715, JT023560, JT023785, JT023822, JT023861 & JT023995

SHEET SIZE:	SCALE:	SHEET NO:
11 X 17	1 : 1	TA-707

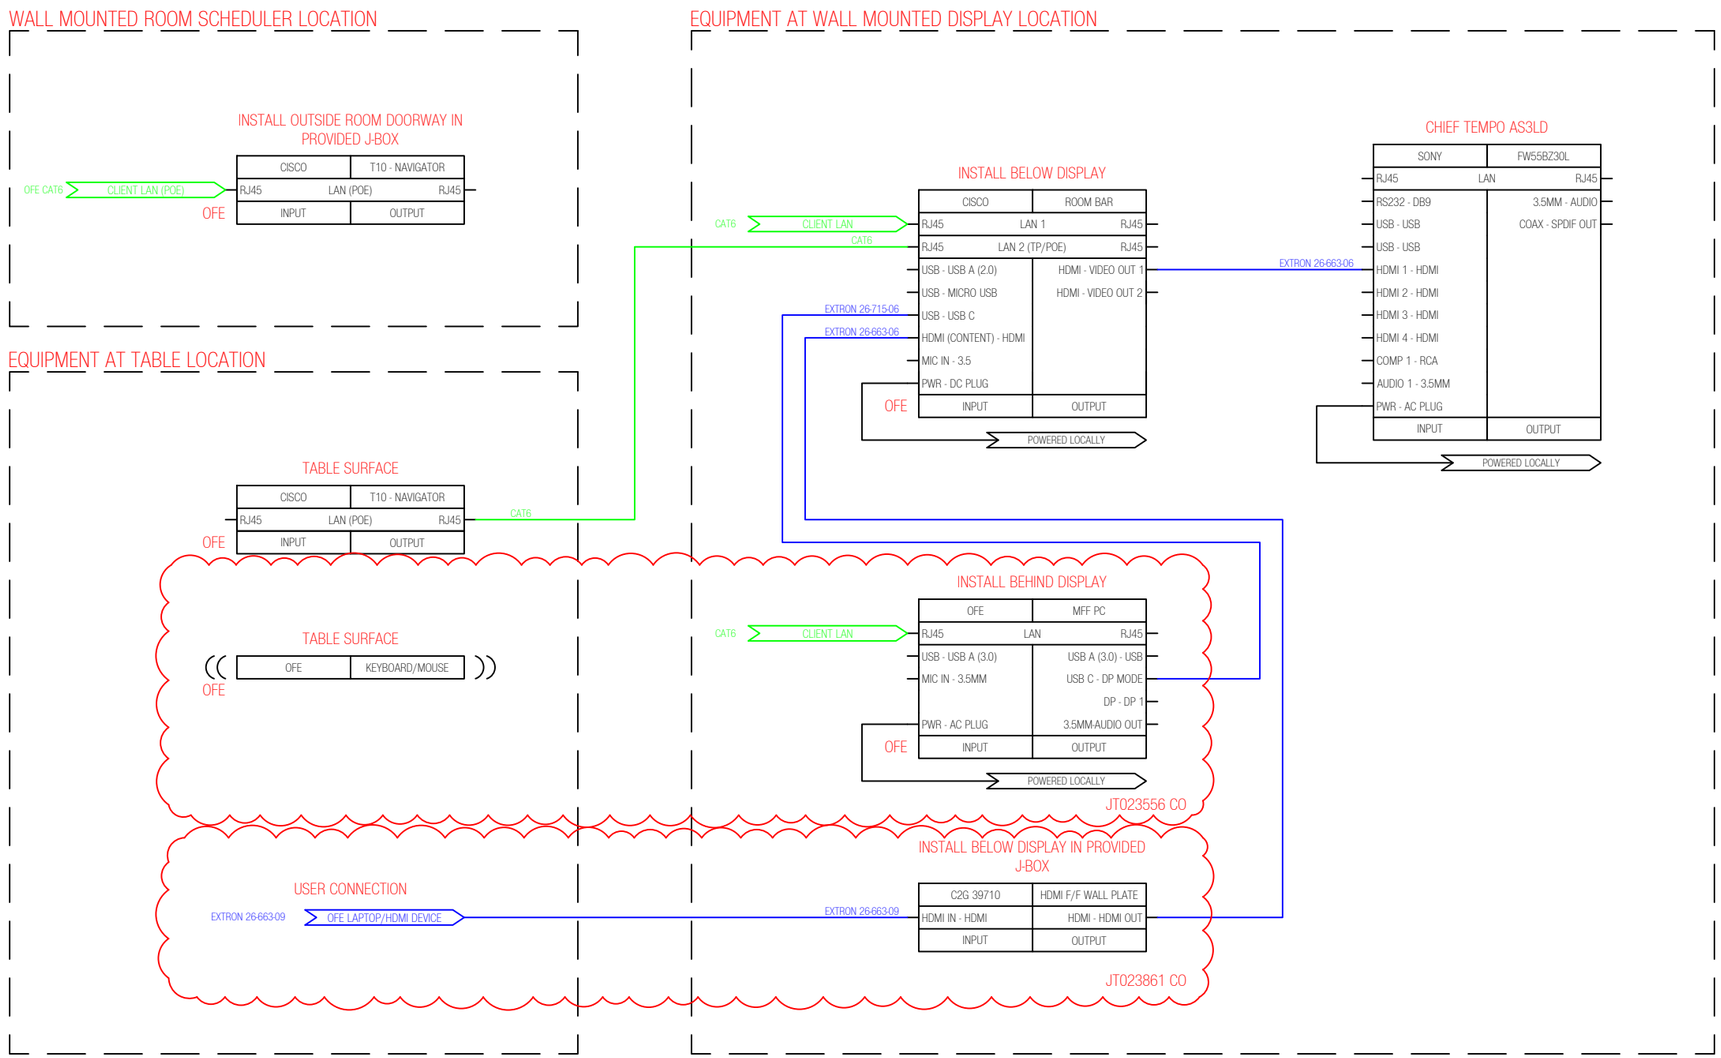

LEAD TECHNICIAN (PRINT): _____

NETWORK REQUIREMENTS			POWER REQUIREMENTS		
QTY	DEVICE	LOCATION	QTY	CIRCUIT/SIZE	LOCATION
1	ROOMBAR	DISPLAY LOCATION	1	15A QUAD	DISPLAY LOCATION
1	ROOM SCHEDULER	OUTSIDE ROOM	-	-	-
1	OFE PC	WALL (BEHIND DISPLAY)	-	-	-
-	-	-	-	-	-
-	-	-	-	-	-
-	-	-	-	-	-
-	-	-	-	-	-
-	-	-	-	-	-
-	-	-	-	-	-
-	-	-	-	-	-

CLIENT NAME: LOCKTON DUNNING

REV:	DATE:	DRAWN BY:
0	03/05/2026	AFS
-	-	-

TAURUS technologies
1420 LAKESIDE PARKWAY, SUITE 100, FLOWER MOUND, TX 75028
WWW.TAURUSTECHINC.COM 1-888-410-5747

ROOM NAME: VICTORY COMMONS - 15TH FLOOR - HUDDLE ROOM 15.044

SITE ADDRESS: 2601 VICTORY AVE, DALLAS, TX 75219

PROJECT NO: JT022715, JT023560, JT023785, JT023822, JT023861 & JT023995

SHEET SIZE:	SCALE:	SHEET NO:
11 X 17	1 : 1	TA-708

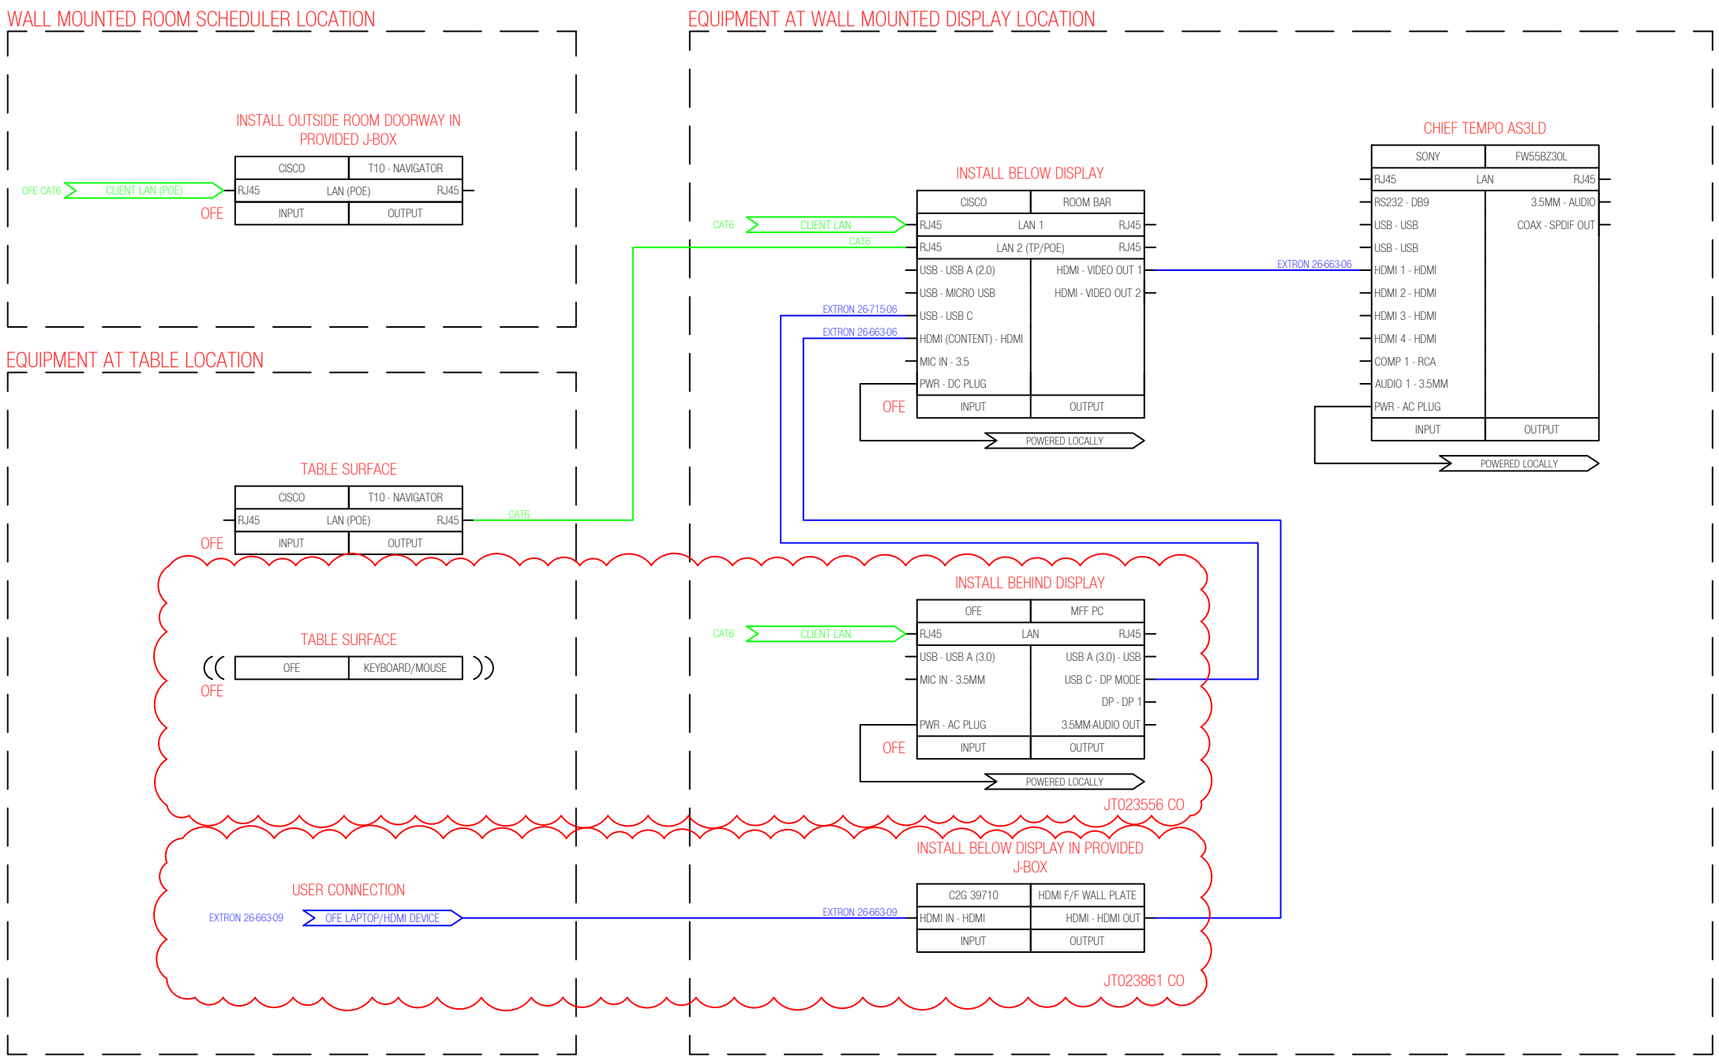

LEAD TECHNICIAN (PRINT): _____

NETWORK REQUIREMENTS			POWER REQUIREMENTS		
QTY	DEVICE	LOCATION	QTY	CIRCUIT/SIZE	LOCATION
1	ROOMBAR	DISPLAY LOCATION	1	15A QUAD	DISPLAY LOCATION
1	ROOM SCHEDULER	OUTSIDE ROOM	-	-	-
1	OFE PC	WALL (BEHIND DISPLAY)	-	-	-
-	-	-	-	-	-
-	-	-	-	-	-
-	-	-	-	-	-
-	-	-	-	-	-
-	-	-	-	-	-
-	-	-	-	-	-
-	-	-	-	-	-

CLIENT NAME: LOCKTON DUNNING

REV:	DATE:	DRAWN BY:
0	03/05/2026	AFS
-	-	-

TAURUS technologies
1420 LAKESIDE PARKWAY, SUITE 100, FLOWER MOUND, TX 75028
WWW.TAURUSTECHINC.COM 1-888-410-5747

ROOM NAME: VICTORY COMMONS - 15TH FLOOR - HUDDLE ROOM 15.094

SITE ADDRESS: 2601 VICTORY AVE, DALLAS, TX 75219

PROJECT NO: JT022715, JT023560, JT023785, JT023822, JT023861 & JT023995

SHEET SIZE:	SCALE:	SHEET NO:
11 X 17	1 : 1	TA-709

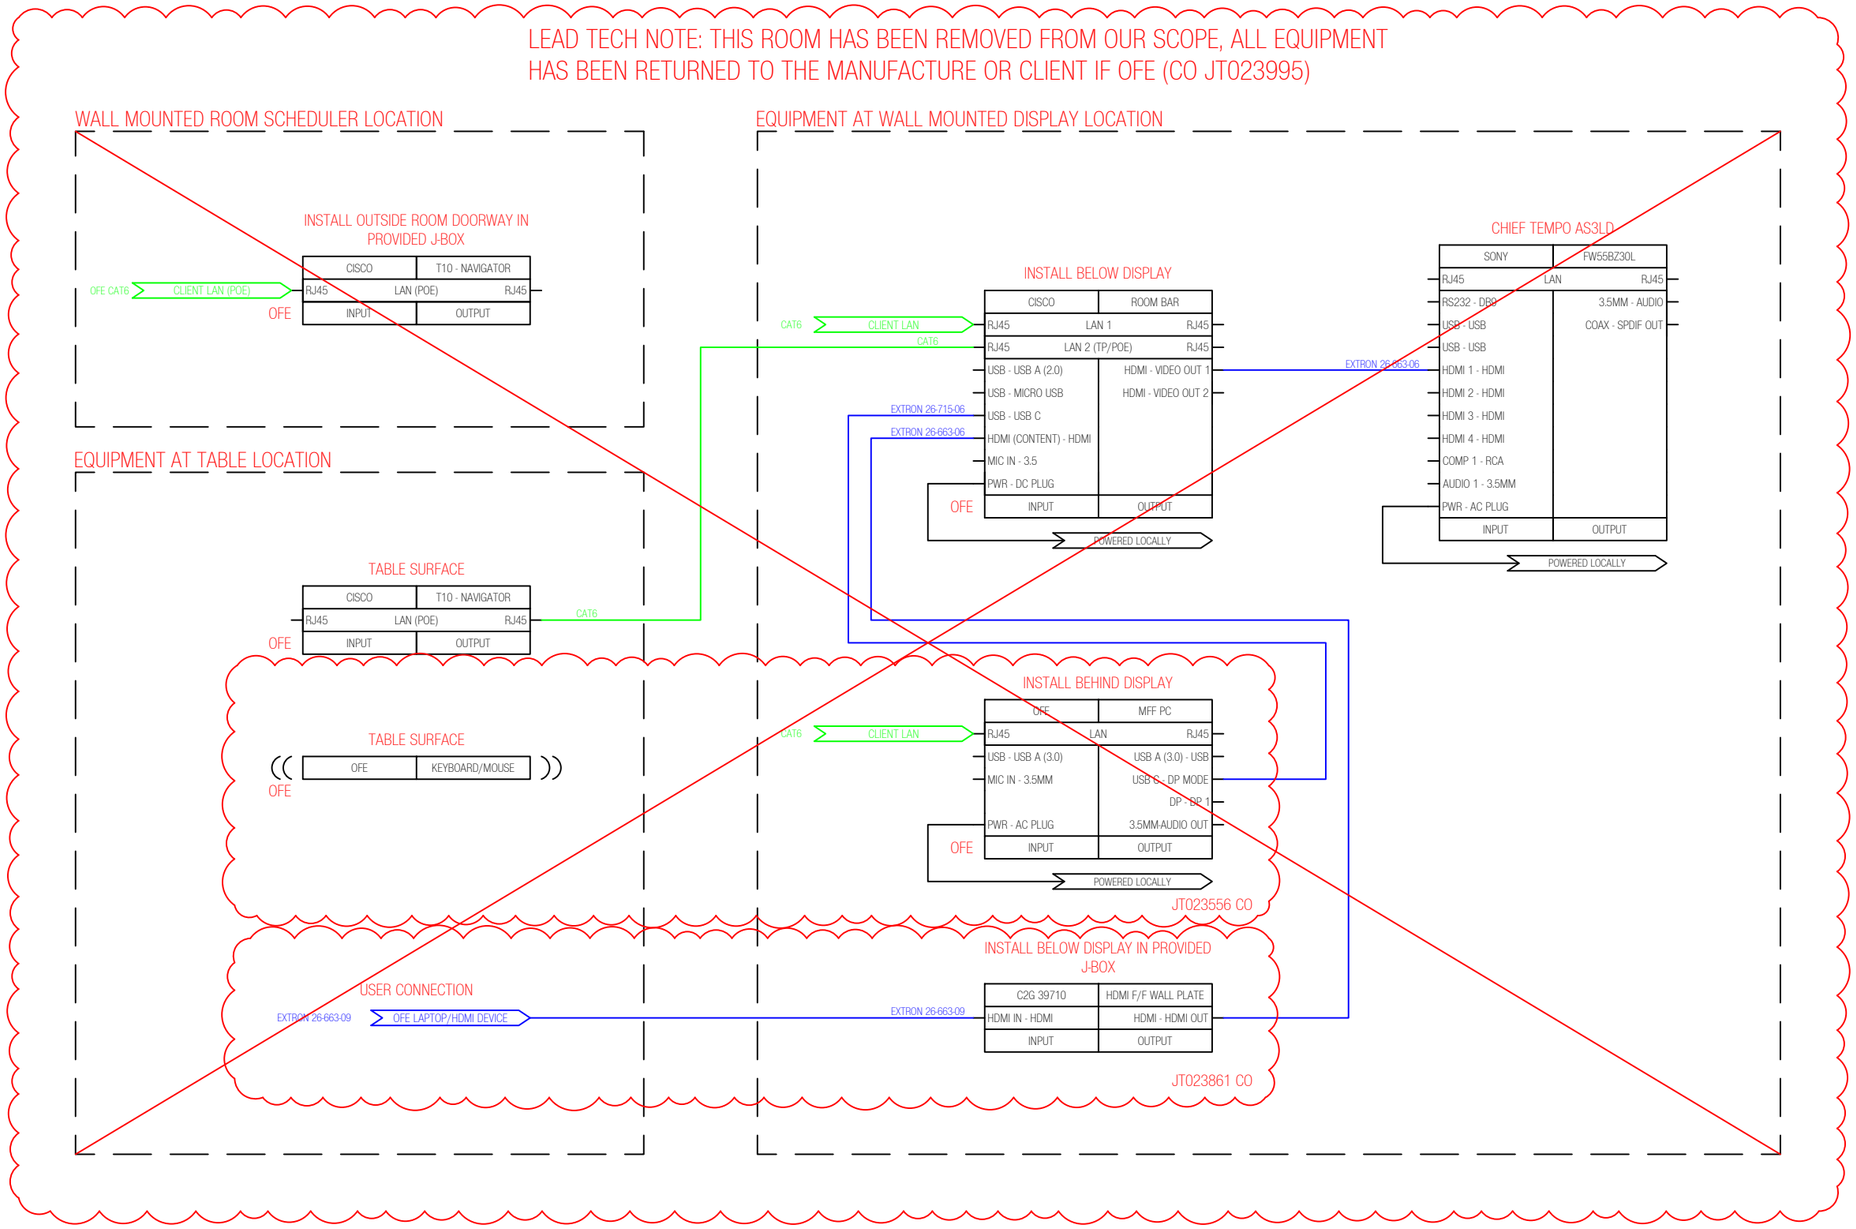

LEAD TECHNICIAN (PRINT): _____

NETWORK REQUIREMENTS			POWER REQUIREMENTS		
QTY	DEVICE	LOCATION	QTY	CIRCUIT/SIZE	LOCATION
1	ROOMBAR	DISPLAY LOCATION	1	15A QUAD	DISPLAY LOCATION
1	ROOM SCHEDULER	OUTSIDE ROOM	-	-	-
1	OFE PC	WALL (BEHIND DISPLAY)	-	-	-
-	-	-	-	-	-
-	-	-	-	-	-
-	-	-	-	-	-
-	-	-	-	-	-
-	-	-	-	-	-
-	-	-	-	-	-
-	-	-	-	-	-

CLIENT NAME: LOCKTON DUNNING

REV:	DATE:	DRAWN BY:
0	03/05/2026	AFS
-	-	-

TAURUS technologies
1420 LAKESIDE PARKWAY, SUITE 100, FLOWER MOUND, TX 75028
WWW.TAURUSTECHINC.COM 1-888-410-5747

ROOM NAME: VICTORY COMMONS - 15TH FLOOR - HUDDLE ROOM 15.105

SITE ADDRESS: 2601 VICTORY AVE, DALLAS, TX 75219

PROJECT NO: JT022715, JT023560, JT023785, JT023822, JT023861 & JT023995

SHEET SIZE:	SCALE:	SHEET NO:
11 X 17	1 : 1	TA-710

LEAD TECH NOTE: THIS ROOM HAS BEEN REMOVED FROM OUR SCOPE, ALL EQUIPMENT HAS BEEN RETURNED TO THE MANUFACTURE OR CLIENT IF OFE (CO JT023995)

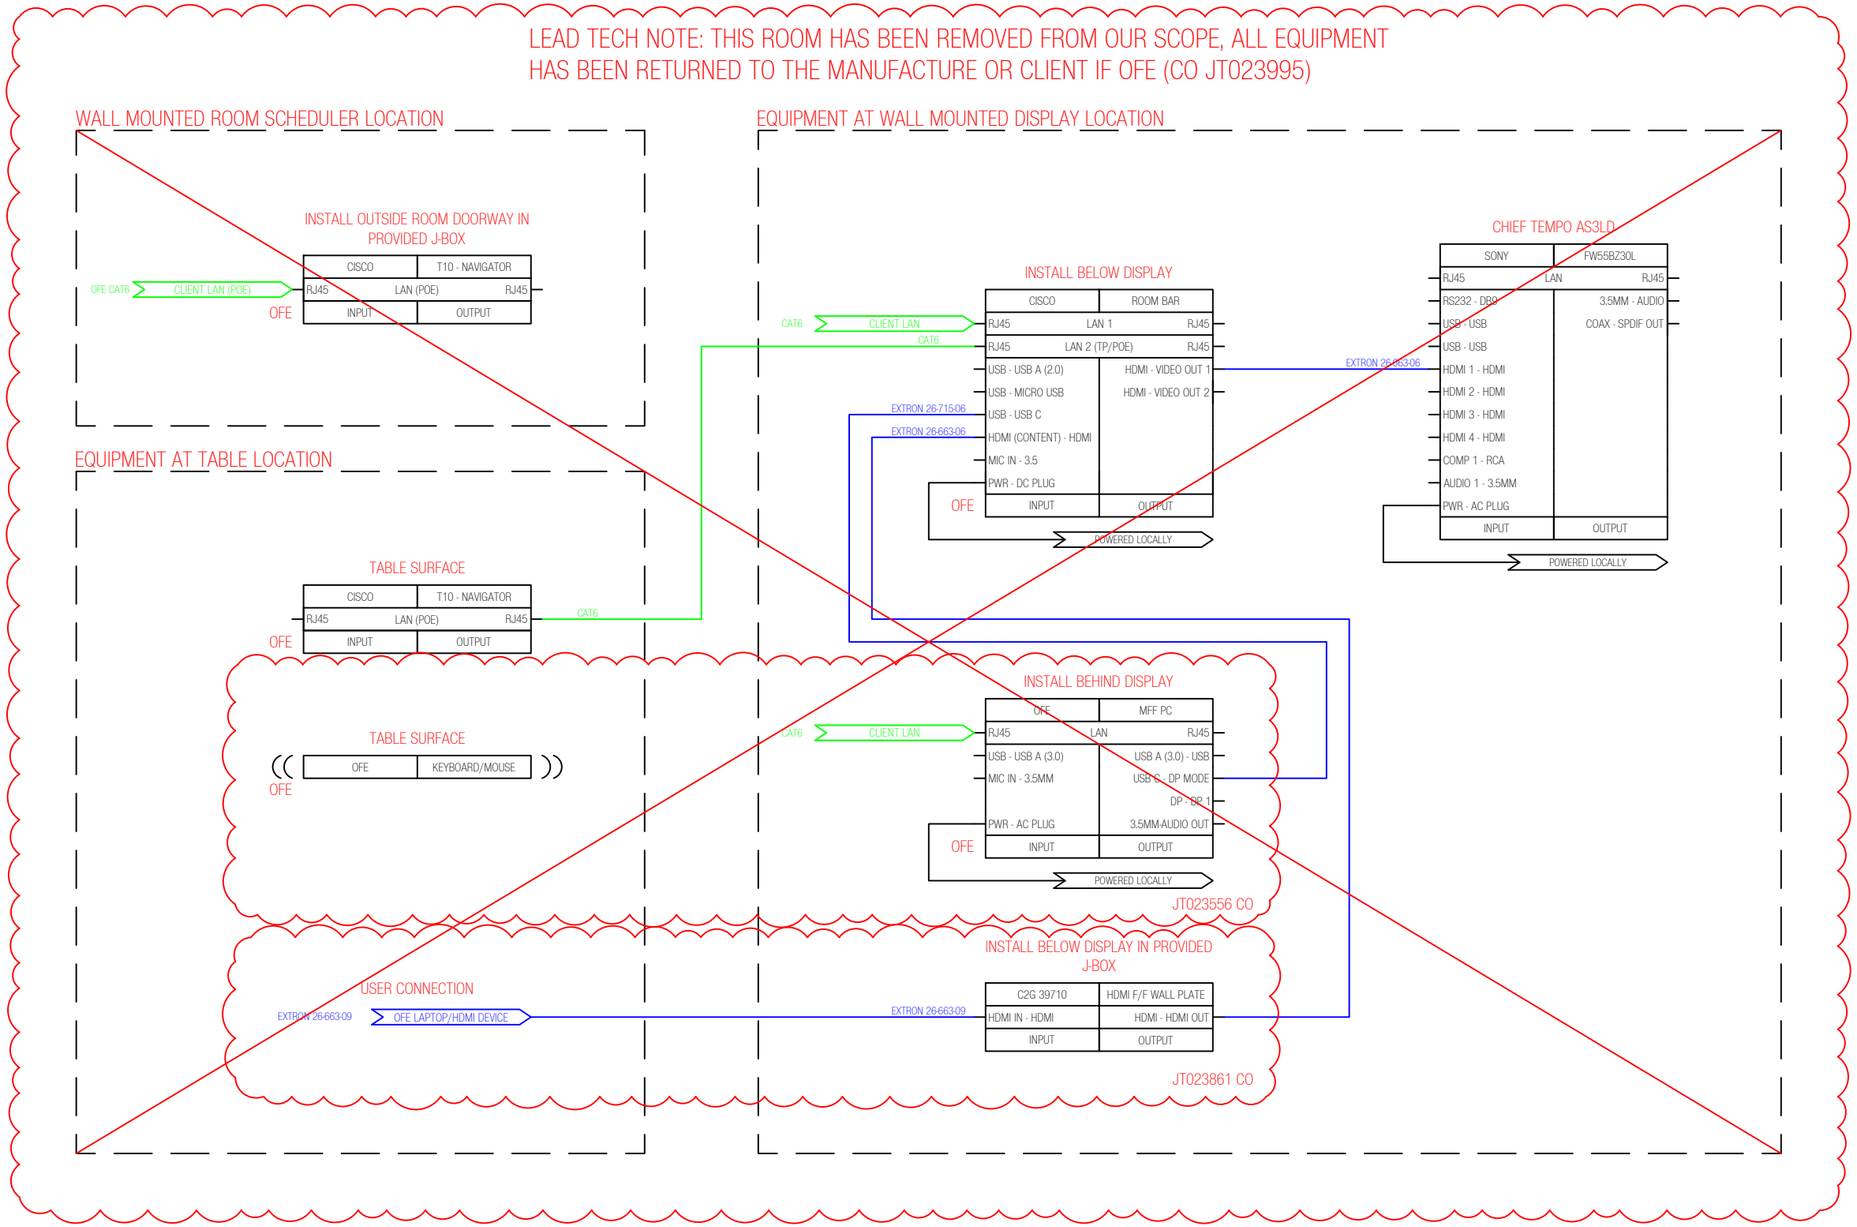

LEAD TECHNICIAN (PRINT): _____

NETWORK REQUIREMENTS			POWER REQUIREMENTS		
QTY	DEVICE	LOCATION	QTY	CIRCUIT/SIZE	LOCATION
1	ROOMBAR	DISPLAY LOCATION	1	15A QUAD	DISPLAY LOCATION
1	ROOM SCHEDULER	OUTSIDE ROOM	-	-	-
1	OFE PC	WALL (BEHIND DISPLAY)	-	-	-
-	-	-	-	-	-
-	-	-	-	-	-
-	-	-	-	-	-
-	-	-	-	-	-
-	-	-	-	-	-
-	-	-	-	-	-
-	-	-	-	-	-

CLIENT NAME: LOCKTON DUNNING

REV:	DATE:	DRAWN BY:
0	03/05/2026	AFS
-	-	-

TAURUS technologies
1420 LAKESIDE PARKWAY, SUITE 100, FLOWER MOUND, TX 75028
WWW.TAURUSTECHINC.COM 1-888-410-5747

ROOM NAME: VICTORY COMMONS - 15TH FLOOR - HUDDLE ROOM 15.106

SITE ADDRESS: 2601 VICTORY AVE, DALLAS, TX 75219

PROJECT NO: JT022715, JT023560, JT023785, JT023822, JT023861 & JT023995

SHEET SIZE:	SCALE:	SHEET NO:
11 X 17	1 : 1	TA-711

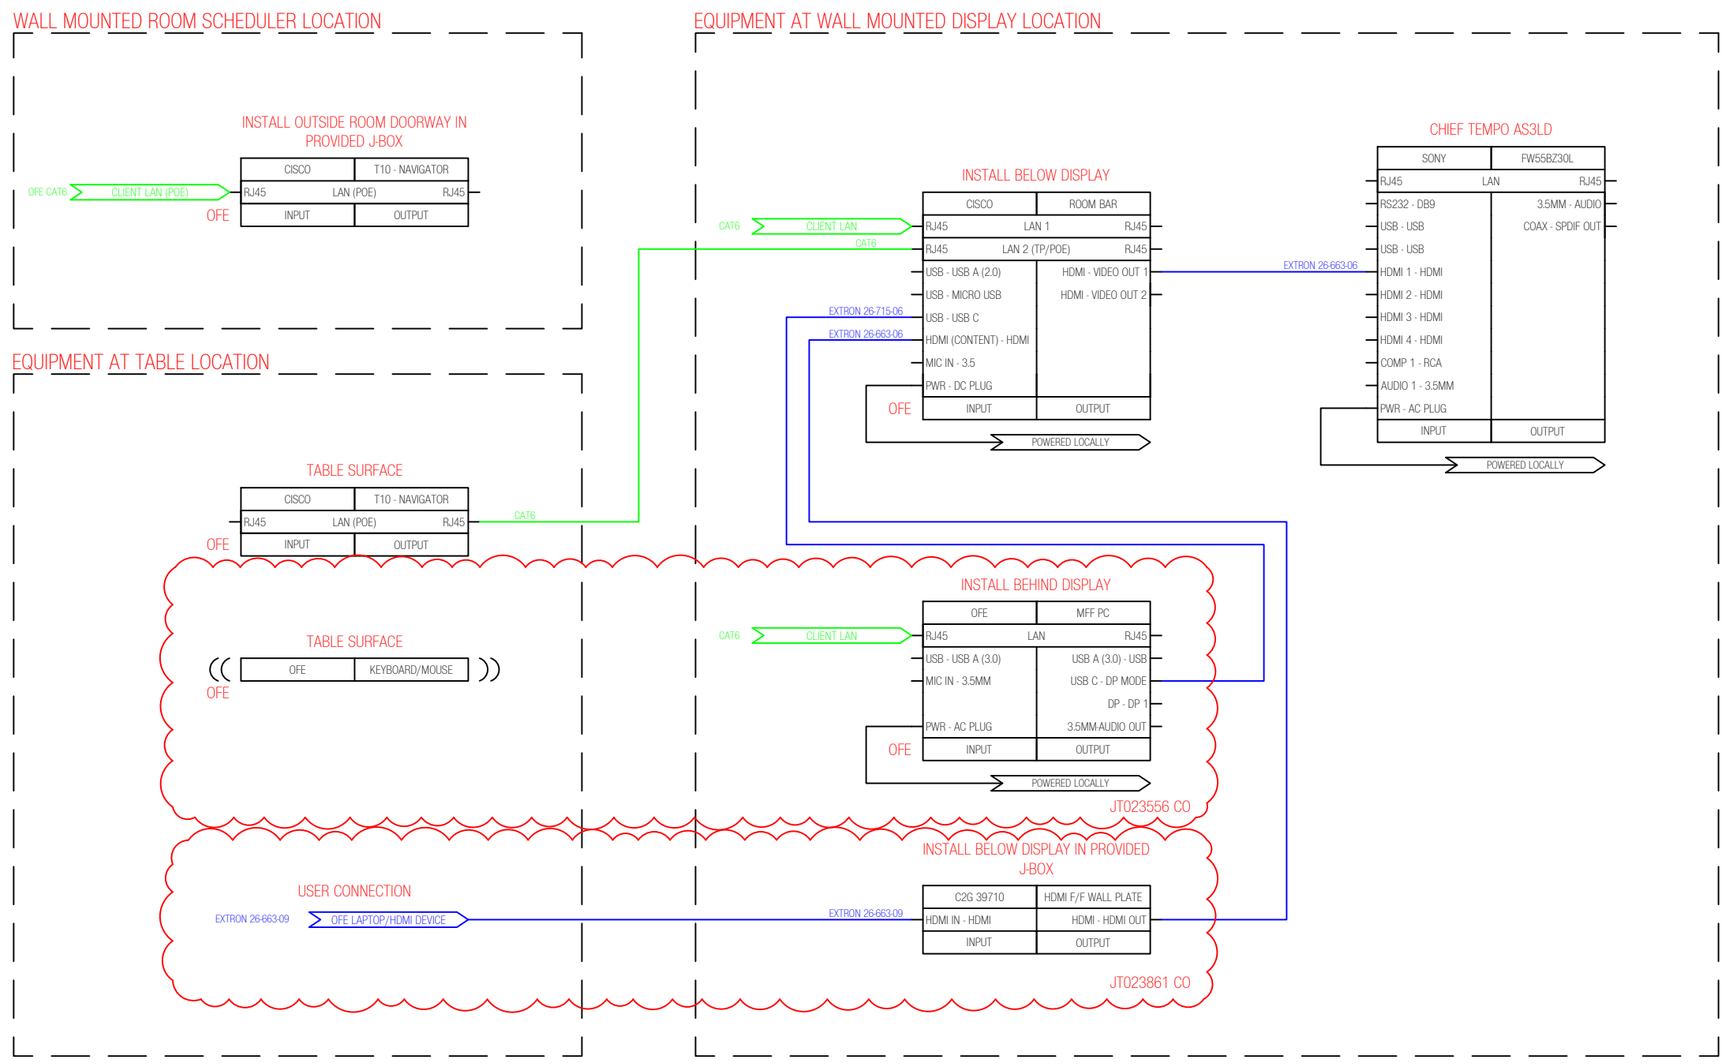

LEAD TECHNICIAN (PRINT): _____

NETWORK REQUIREMENTS			POWER REQUIREMENTS		
QTY	DEVICE	LOCATION	QTY	CIRCUIT/SIZE	LOCATION
1	ROOMBAR	DISPLAY LOCATION	1	15A QUAD	DISPLAY LOCATION
1	ROOM SCHEDULER	OUTSIDE ROOM	-	-	-
1	OFE PC	WALL (BEHIND DISPLAY)	-	-	-
-	-	-	-	-	-
-	-	-	-	-	-
-	-	-	-	-	-
-	-	-	-	-	-
-	-	-	-	-	-
-	-	-	-	-	-
-	-	-	-	-	-

CLIENT NAME: LOCKTON DUNNING

REV:	DATE:	DRAWN BY:
0	03/05/2026	AFS
-	-	-

TAURUS technologies
1420 LAKESIDE PARKWAY, SUITE 100, FLOWER MOUND, TX 75028
WWW.TAURUSTECHINC.COM 1-888-410-5747

ROOM NAME: VICTORY COMMONS - 15TH FLOOR - HUDDLE ROOM 15.115

SITE ADDRESS: 2601 VICTORY AVE, DALLAS, TX 75219

PROJECT NO: JT022715, JT023560, JT023785, JT023822, JT023861 & JT023995

SHEET SIZE:	SCALE:	SHEET NO:
11 X 17	1 : 1	TA-712

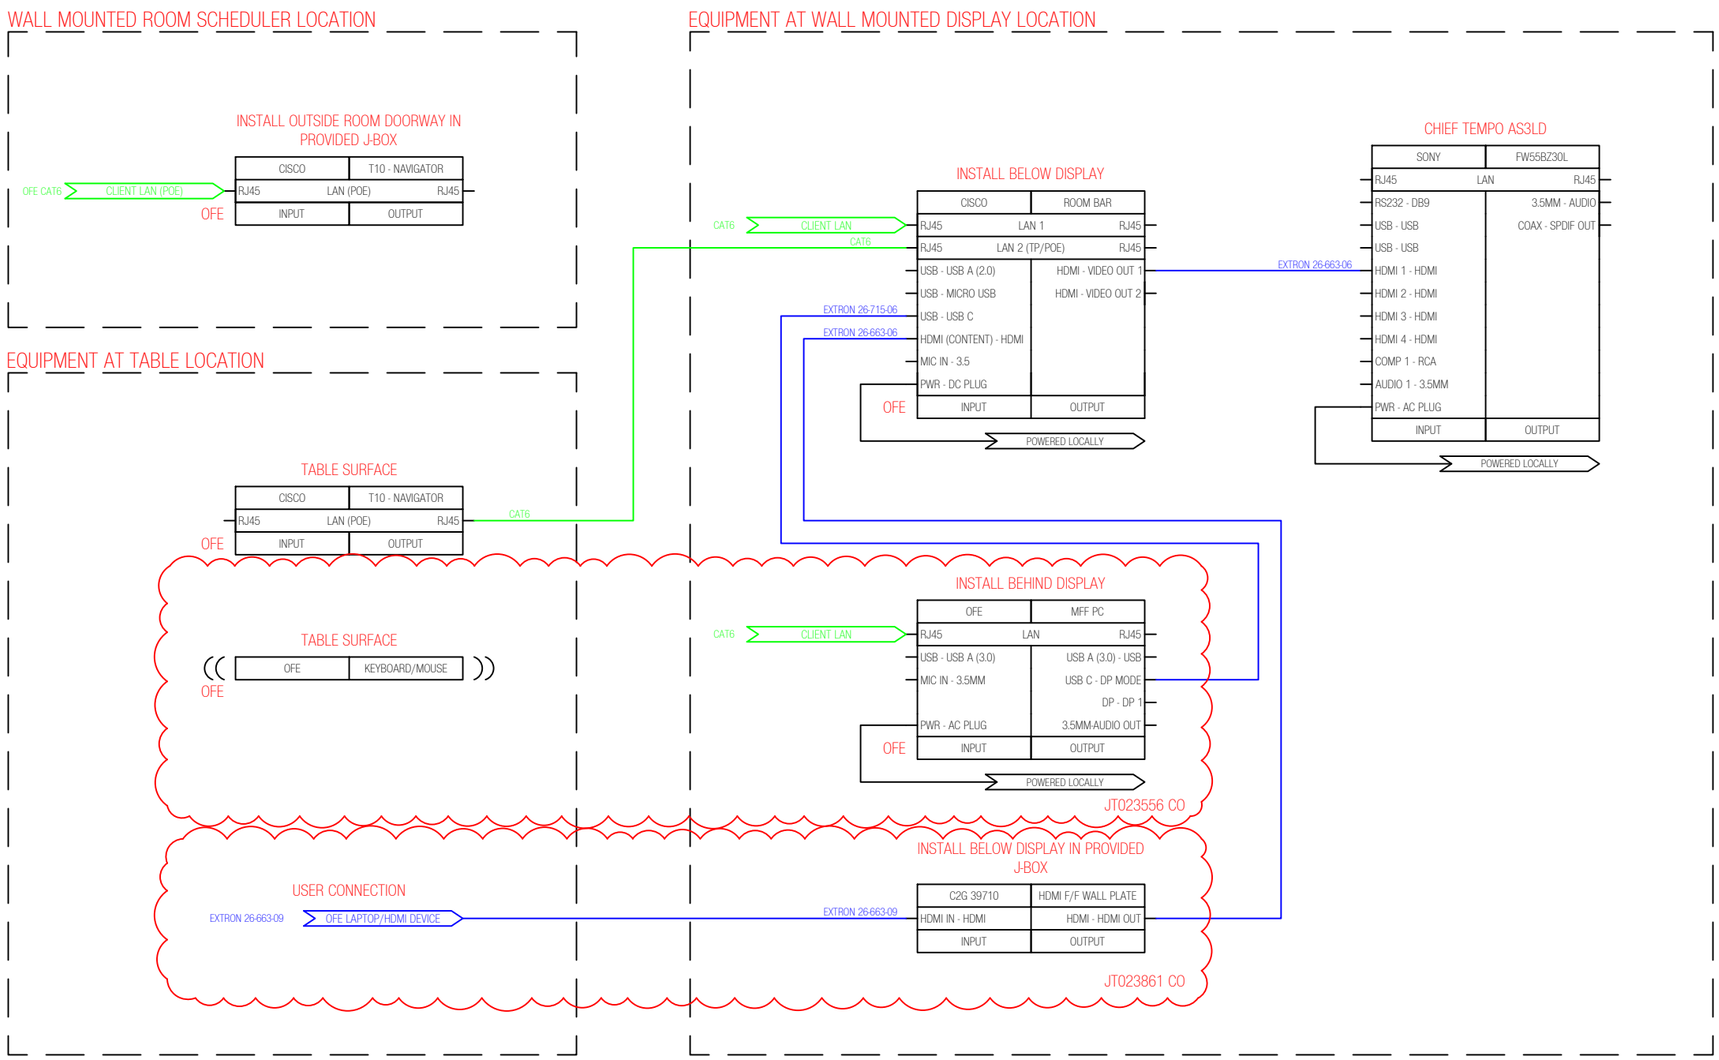

LEAD TECHNICIAN (PRINT): _____

NETWORK REQUIREMENTS			POWER REQUIREMENTS		
QTY	DEVICE	LOCATION	QTY	CIRCUIT/SIZE	LOCATION
1	ROOMBAR	DISPLAY LOCATION	1	15A QUAD	DISPLAY LOCATION
1	ROOM SCHEDULER	OUTSIDE ROOM	-	-	-
1	OFE PC	WALL (BEHIND DISPLAY)	-	-	-
-	-	-	-	-	-
-	-	-	-	-	-
-	-	-	-	-	-
-	-	-	-	-	-
-	-	-	-	-	-
-	-	-	-	-	-
-	-	-	-	-	-

CLIENT NAME: LOCKTON DUNNING

REV:	DATE:	DRAWN BY:
0	03/05/2026	AFS
-	-	-

TAURUS technologies
1420 LAKESIDE PARKWAY, SUITE 100, FLOWER MOUND, TX 75028
WWW.TAURUSTECHINC.COM 1-888-410-5747

ROOM NAME: VICTORY COMMONS - 15TH FLOOR - HUDDLE ROOM 15.116

SITE ADDRESS: 2601 VICTORY AVE, DALLAS, TX 75219

PROJECT NO: JT022715, JT023560, JT023785, JT023822, JT023861 & JT023995

SHEET SIZE:	SCALE:	SHEET NO:
11 X 17	1 : 1	TA-713

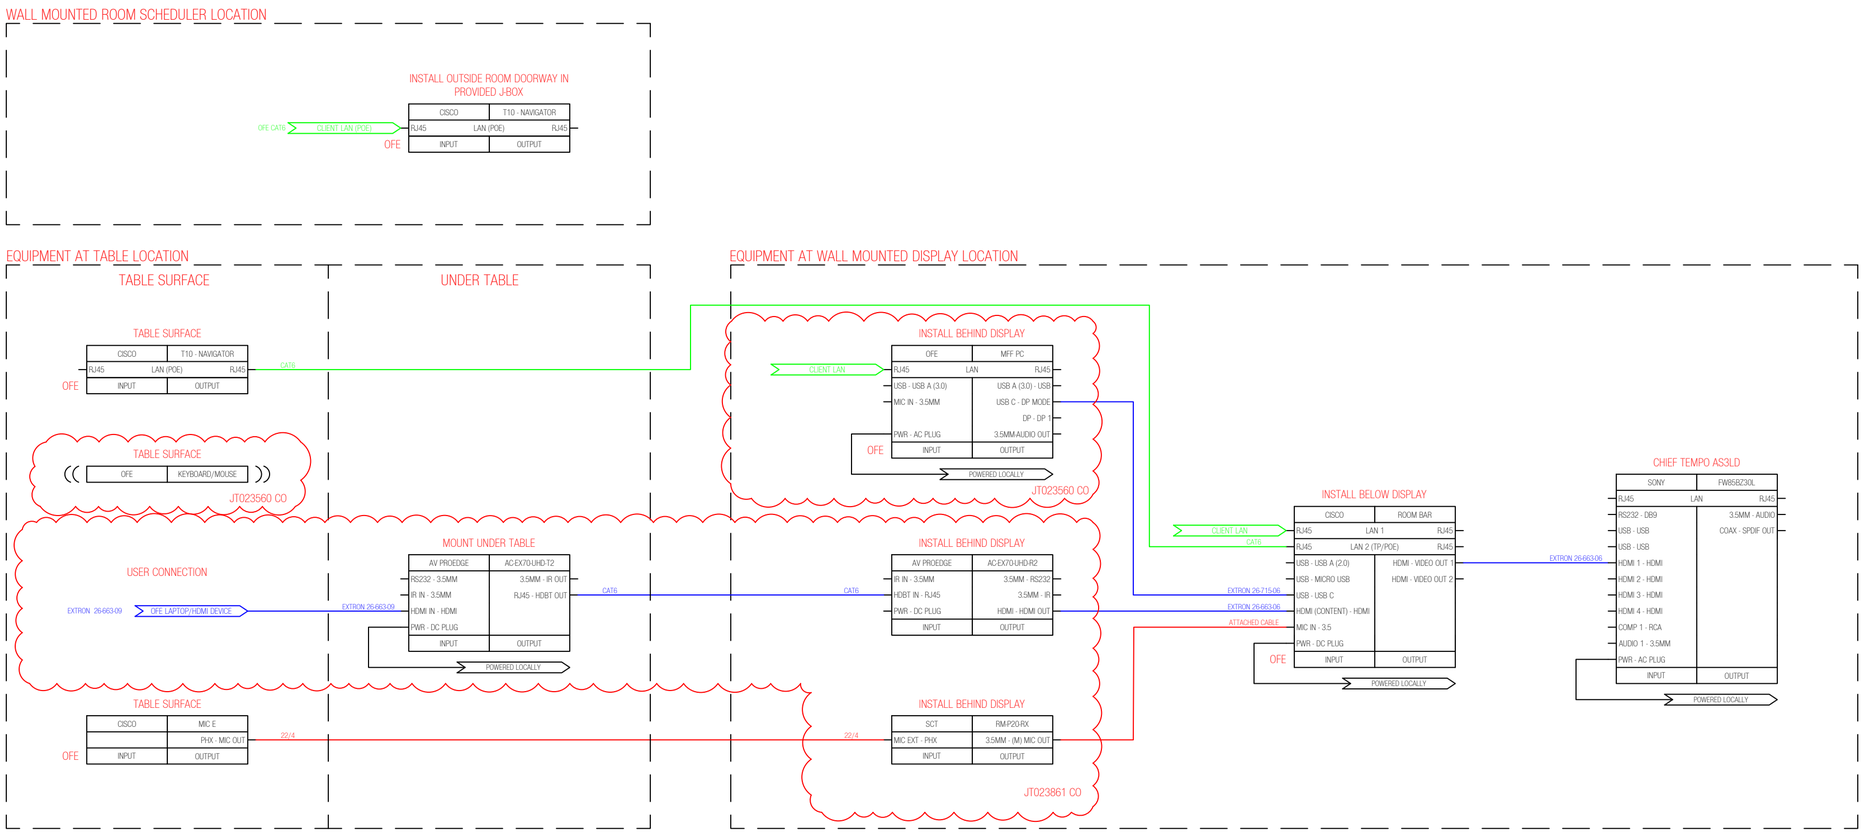

LEAD TECHNICIAN (PRINT): _____

NETWORK REQUIREMENTS			POWER REQUIREMENTS		
QTY	DEVICE	LOCATION	QTY	CIRCUIT/SIZE	LOCATION
1	ROOMBAR	DISPLAY LOCATION	1	15A QUAD	DISPLAY LOCATION
1	ROOM SCHEDULER	OUTSIDE ROOM	1	15A DUPLEX	TABLE LOCATION
1	OFE PC	WALL (BEHIND DISPLAY)	-	-	-
-	-	-	-	-	-
-	-	-	-	-	-
-	-	-	-	-	-
-	-	-	-	-	-
-	-	-	-	-	-
-	-	-	-	-	-
-	-	-	-	-	-
-	-	-	-	-	-

CLIENT NAME: LOCKTON DUNNING

REV:	DATE:	DRAWN BY:
0	03/05/2026	AFS
-	-	-

TAURUS technologies
1420 LAKESIDE PARKWAY, SUITE 100, FLOWER MOUND, TX 75028
WWW.TAURUSTECHINC.COM 1-888-410-5747

ROOM NAME: VICTORY COMMONS - 14TH FL - SMALL (MEDIUM) CONF RM 14.188

SITE ADDRESS: 2601 VICTORY AVE, DALLAS, TX 75219

PROJECT NO: JT022715, JT023560, JT023785, JT023822, JT023861 & JT023995

SHEET SIZE:	SCALE:	SHEET NO:
11 X 17	1 : 1	TA-714

EQUIPMENT AT WALL MOUNTED DISPLAY LOCATION

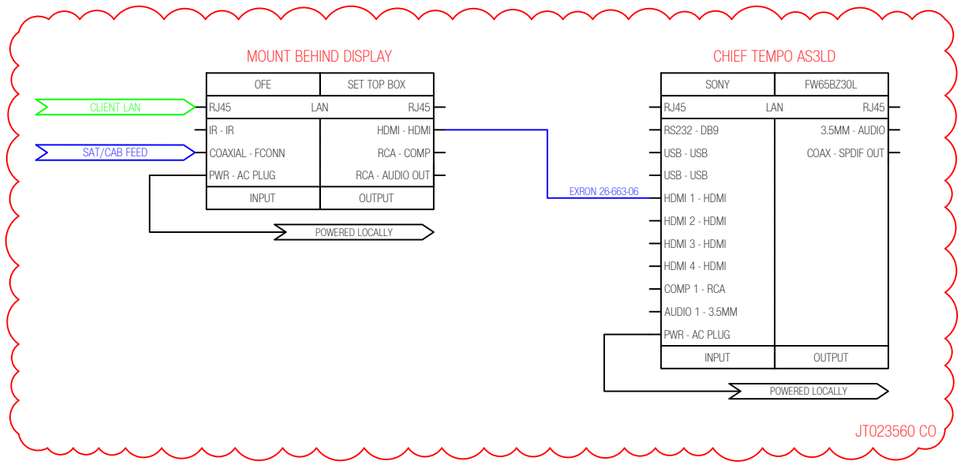

LEAD TECHNICIAN (PRINT): _____

NETWORK REQUIREMENTS			POWER REQUIREMENTS		
QTY	DEVICE	LOCATION	QTY	CIRCUIT/SIZE	LOCATION
1	OFE SET TOP BOX	WALL (BEHIND DISPLAY)	1	15A DUPLEX	WALL (BEHIND DISPLAY)
-	-	-	-	-	-
-	-	-	-	-	-
-	-	-	-	-	-
-	-	-	-	-	-
-	-	-	-	-	-
-	-	-	-	-	-
-	-	-	-	-	-
-	-	-	-	-	-
-	-	-	-	-	-

CLIENT NAME: LOCKTON DUNNING

REV:	DATE:	DRAWN BY:
0	03/05/2026	AFS
-	-	-

TAURUS technologies
1420 LAKESIDE PARKWAY, SUITE 100, FLOWER MOUND, TX 75028
WWW.TAURUSTECHINC.COM 1-888-410-5747

ROOM NAME: VICTORY COMMONS - 15TH FL - COLLABORATION RM 15.070

SITE ADDRESS: 2601 VICTORY AVE, DALLAS, TX 75219

PROJECT NO: JT022715, JT023560, JT023785, JT023822, JT023861 & JT023995

SHEET SIZE:	SCALE:	SHEET NO:
11 X 17	1 : 1	TA-715

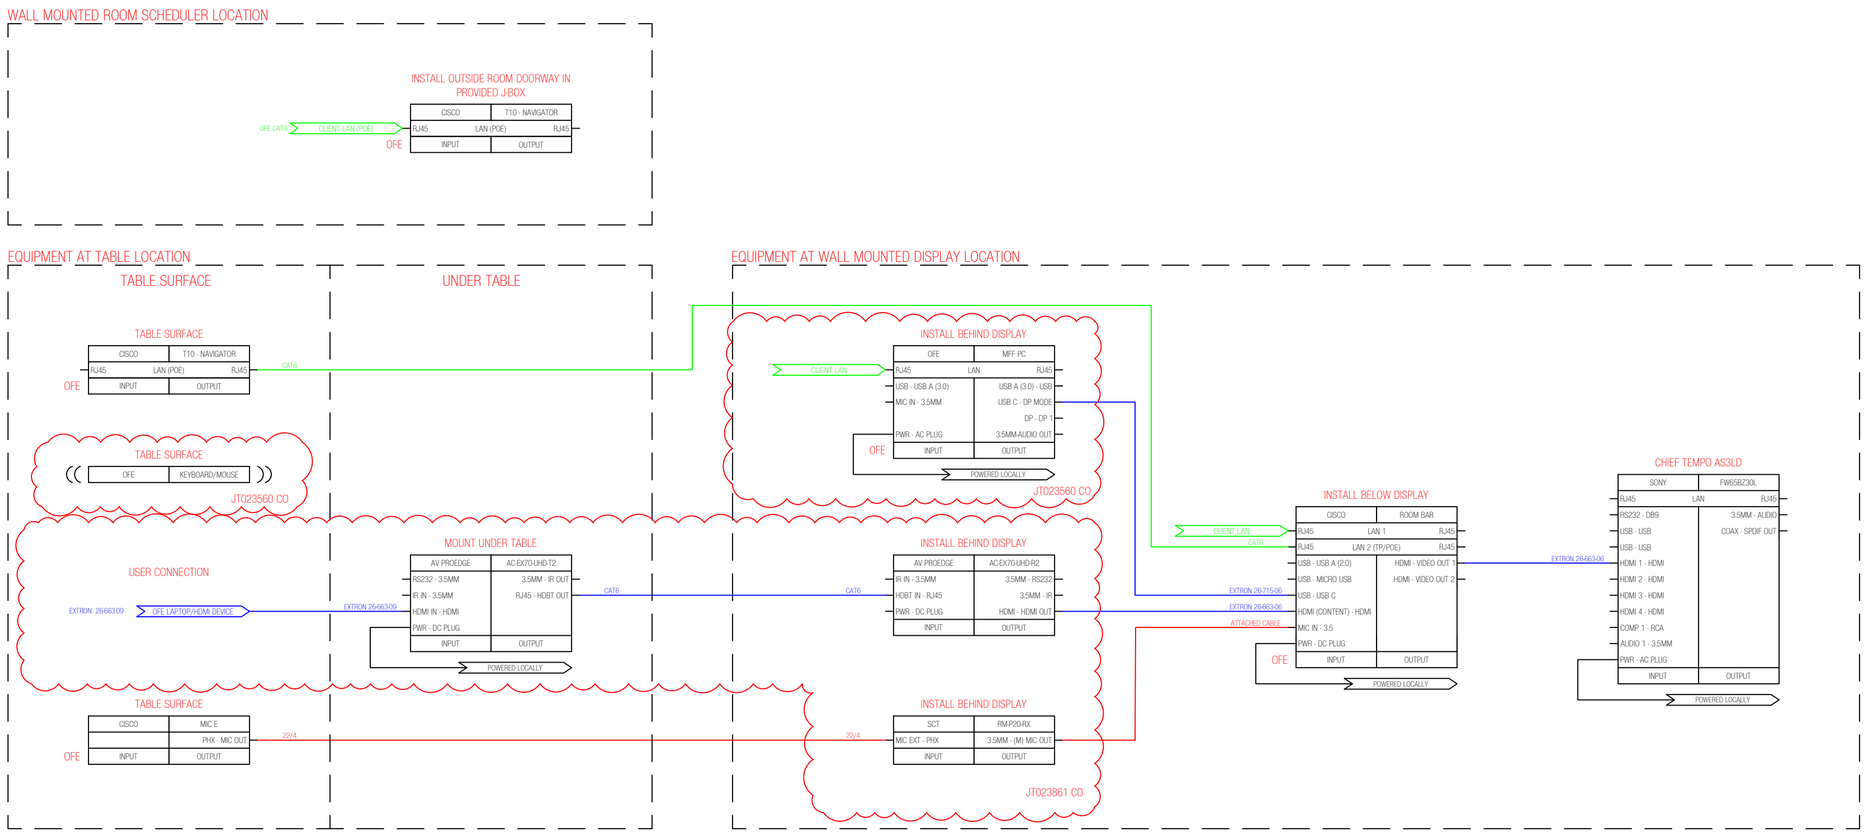

LEAD TECHNICIAN (PRINT): _____

NETWORK REQUIREMENTS			POWER REQUIREMENTS		
QTY	DEVICE	LOCATION	QTY	CIRCUIT/SIZE	LOCATION
1	ROOMBAR	DISPLAY LOCATION	1	15A QUAD	DISPLAY LOCATION
1	ROOM SCHEDULER	OUTSIDE ROOM	1	15A DUPLEX	TABLE LOCATION
1	OFE PC	WALL (BEHIND DISPLAY)	-	-	-
-	-	-	-	-	-
-	-	-	-	-	-
-	-	-	-	-	-
-	-	-	-	-	-
-	-	-	-	-	-
-	-	-	-	-	-
-	-	-	-	-	-

CLIENT NAME: LOCKTON DUNNING

REV:	DATE:	DRAWN BY:
0	03/05/2026	AFS
-	-	-

TAURUS technologies
1420 LAKESIDE PARKWAY, SUITE 100, FLOWER MOUND, TX 75028
WWW.TAURUSTECHINC.COM 1-888-410-5747

ROOM NAME: VICTORY COMMONS - 15TH FL - SMALL (MEDIUM) CONF RM 15.071

SITE ADDRESS: 2601 VICTORY AVE, DALLAS, TX 75219

PROJECT NO: JT022715, JT023560, JT023785, JT023822, JT023861 & JT023995

SHEET SIZE:	SCALE:	SHEET NO:
11 X 17	1 : 1	TA-716

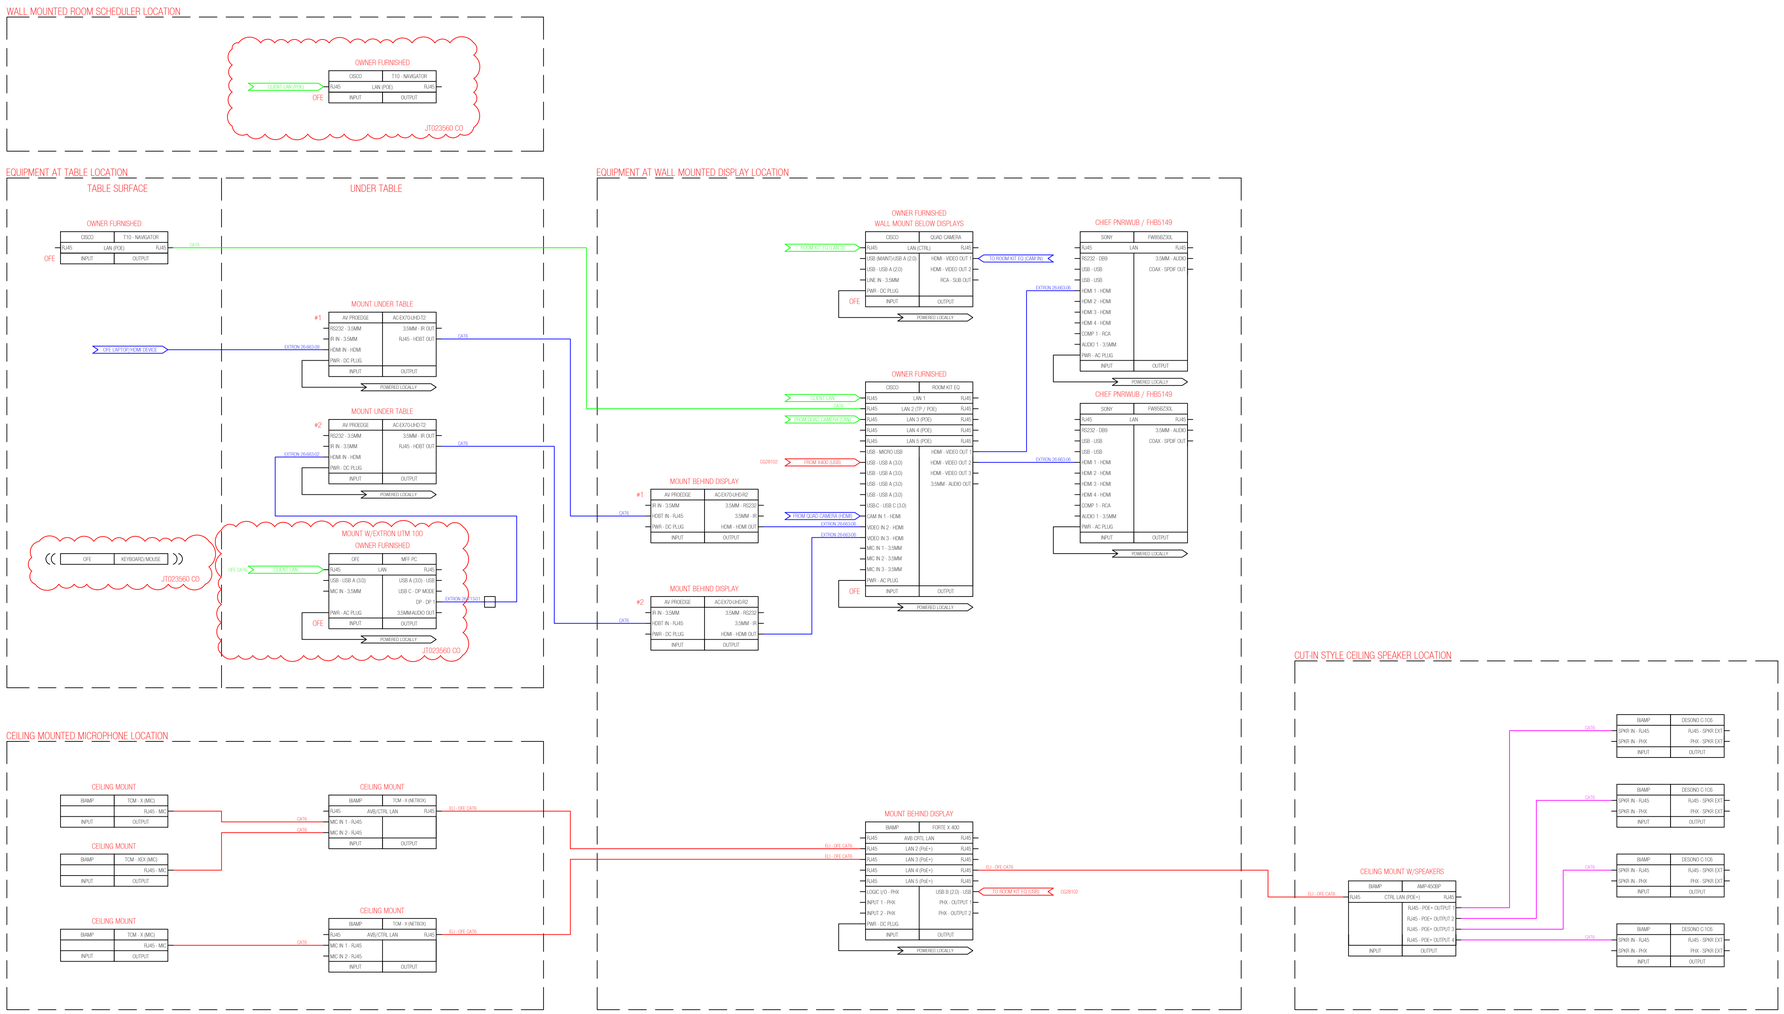

NETWORK REQUIREMENTS			POWER REQUIREMENTS		
QTY	DEVICE	LOCATION	QTY	CIRCUIT/SIZE	LOCATION
1	ROOMKIT EQ	DISPLAY LOCATION	1	15A QUAD	DISPLAY LOCATION
1	ROOM SCHEDULER	OUTSIDE ROOM	1	15A QUAD	TABLE LOCATION
1	OFE PC	FLOOR (CONF. TABLE)	-	-	-
-	-	-	-	-	-
-	-	-	-	-	-
-	-	-	-	-	-
-	-	-	-	-	-
-	-	-	-	-	-
-	-	-	-	-	-
-	-	-	-	-	-
-	-	-	-	-	-

CLIENT NAME:

LOCKTON DUNNING

REV:	DATE:	DRAWN BY:
0	03/05/2026	AFS
		-

TAURUS technologies
1420 LAKESIDE PARKWAY, SUITE 100, FLOWER MOUND, TX 75028
WWW.TAURUSTECHINC.COM 1-888-410-5747

LEAD TECHNICIAN (PRINT): _____

ROOM NAME: VICTORY COMMONS - 14TH FLOOR - ELEVATED CONF RM 14.095

SITE ADDRESS: 2601 VICTORY AVE, DALLAS, TX 75219

PROJECT NO: JT022715, JT023560, JT023785, JT023822, JT023861 & JT023995

SHEET SIZE:	SCALE:	SHEET NO:
24 X 36	1 : 1	TA-717

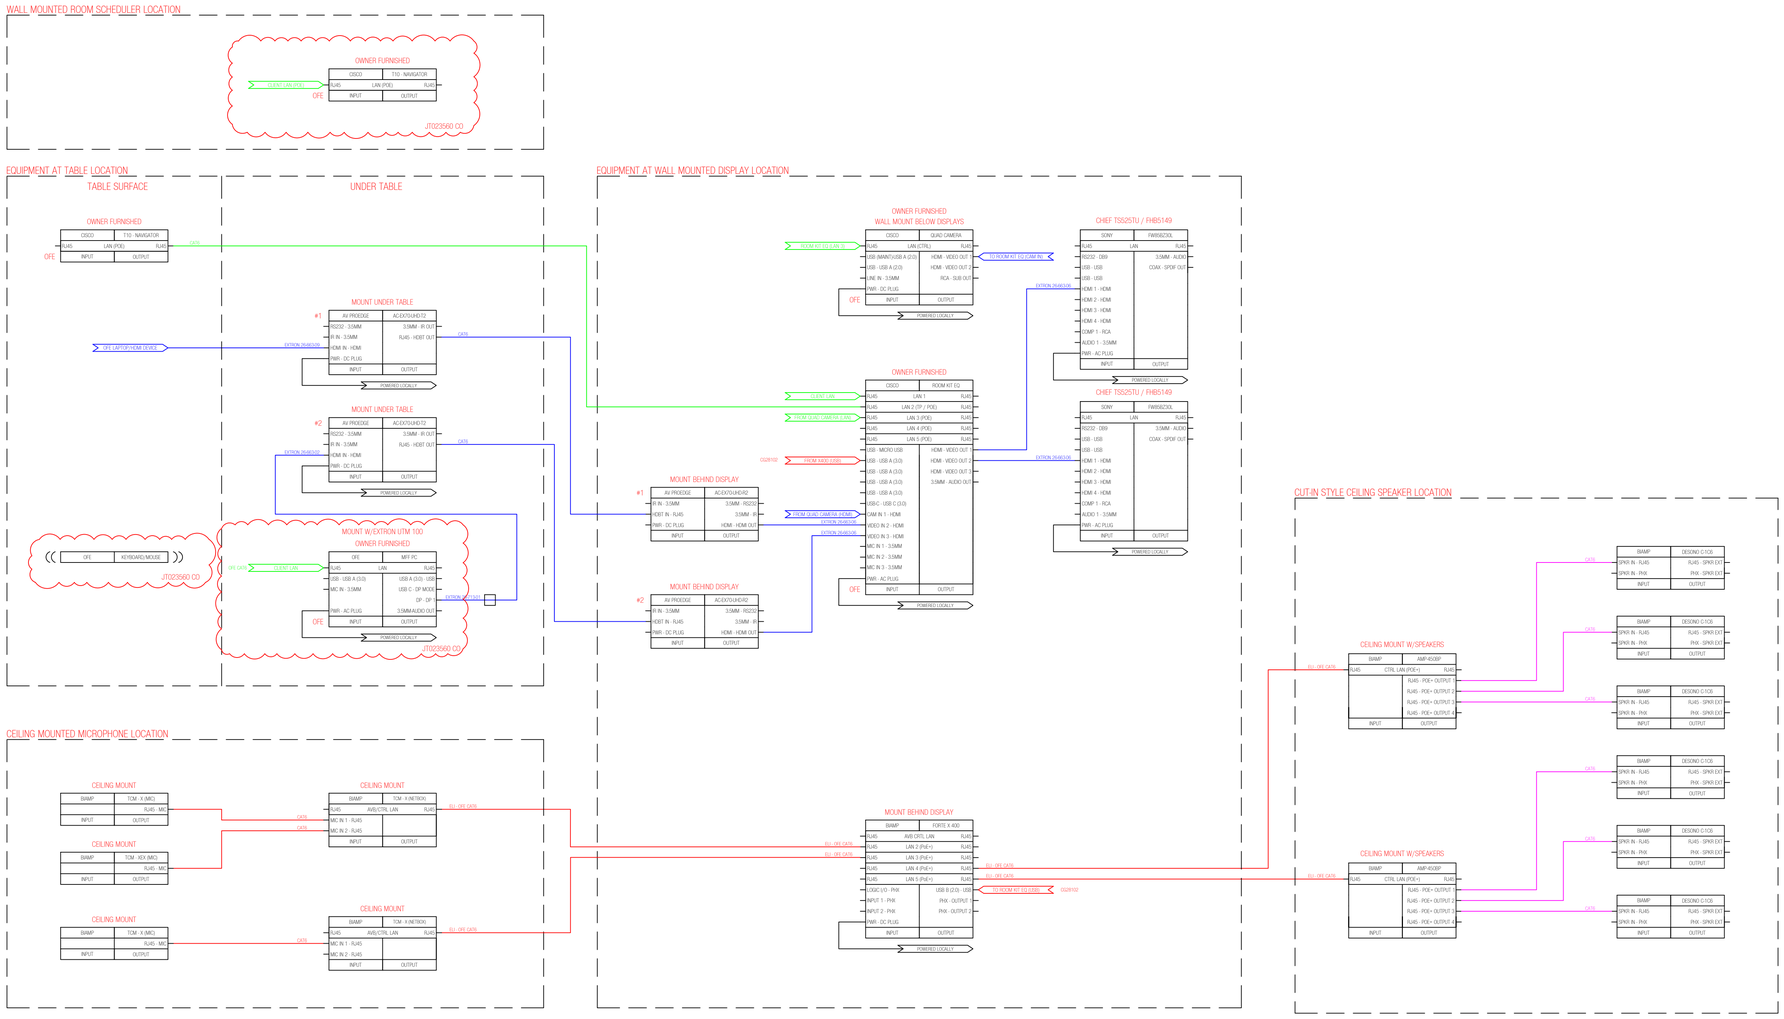

NETWORK REQUIREMENTS			POWER REQUIREMENTS		
QTY	DEVICE	LOCATION	QTY	CIRCUIT/SIZE	LOCATION
1	ROOMKIT EQ	DISPLAY LOCATION	1	15A QUAD	DISPLAY LOCATION
1	ROOM SCHEDULER	OUTSIDE ROOM	1	15A QUAD	TABLE LOCATION
1	OFE PC	FLOOR (CONF. TABLE)	-	-	-
-	-	-	-	-	-
-	-	-	-	-	-
-	-	-	-	-	-
-	-	-	-	-	-
-	-	-	-	-	-
-	-	-	-	-	-
-	-	-	-	-	-
-	-	-	-	-	-

CLIENT NAME:
LOCKTON DUNNING

REV:	DATE:	DRAWN BY:
0	03/05/2026	AFS
-	-	-

TAURUS technologies
1420 LAKESIDE PARKWAY, SUITE 100, FLOWER MOUND, TX 75028
WWW.TAURUSTECHINC.COM 1-888-410-5747

LEAD TECHNICIAN (PRINT): _____

ROOM NAME: VICTORY COMMONS - 15TH FLOOR - ELEVATED CONF ROOM 15.083

SITE ADDRESS: 2601 VICTORY AVE, DALLAS, TX 75219

PROJECT NO: JT022715, JT023560, JT023785, JT023822, JT023861 & JT023995

SHEET SIZE:	SCALE:	SHEET NO:
24 X 36	1 : 1	TA-718

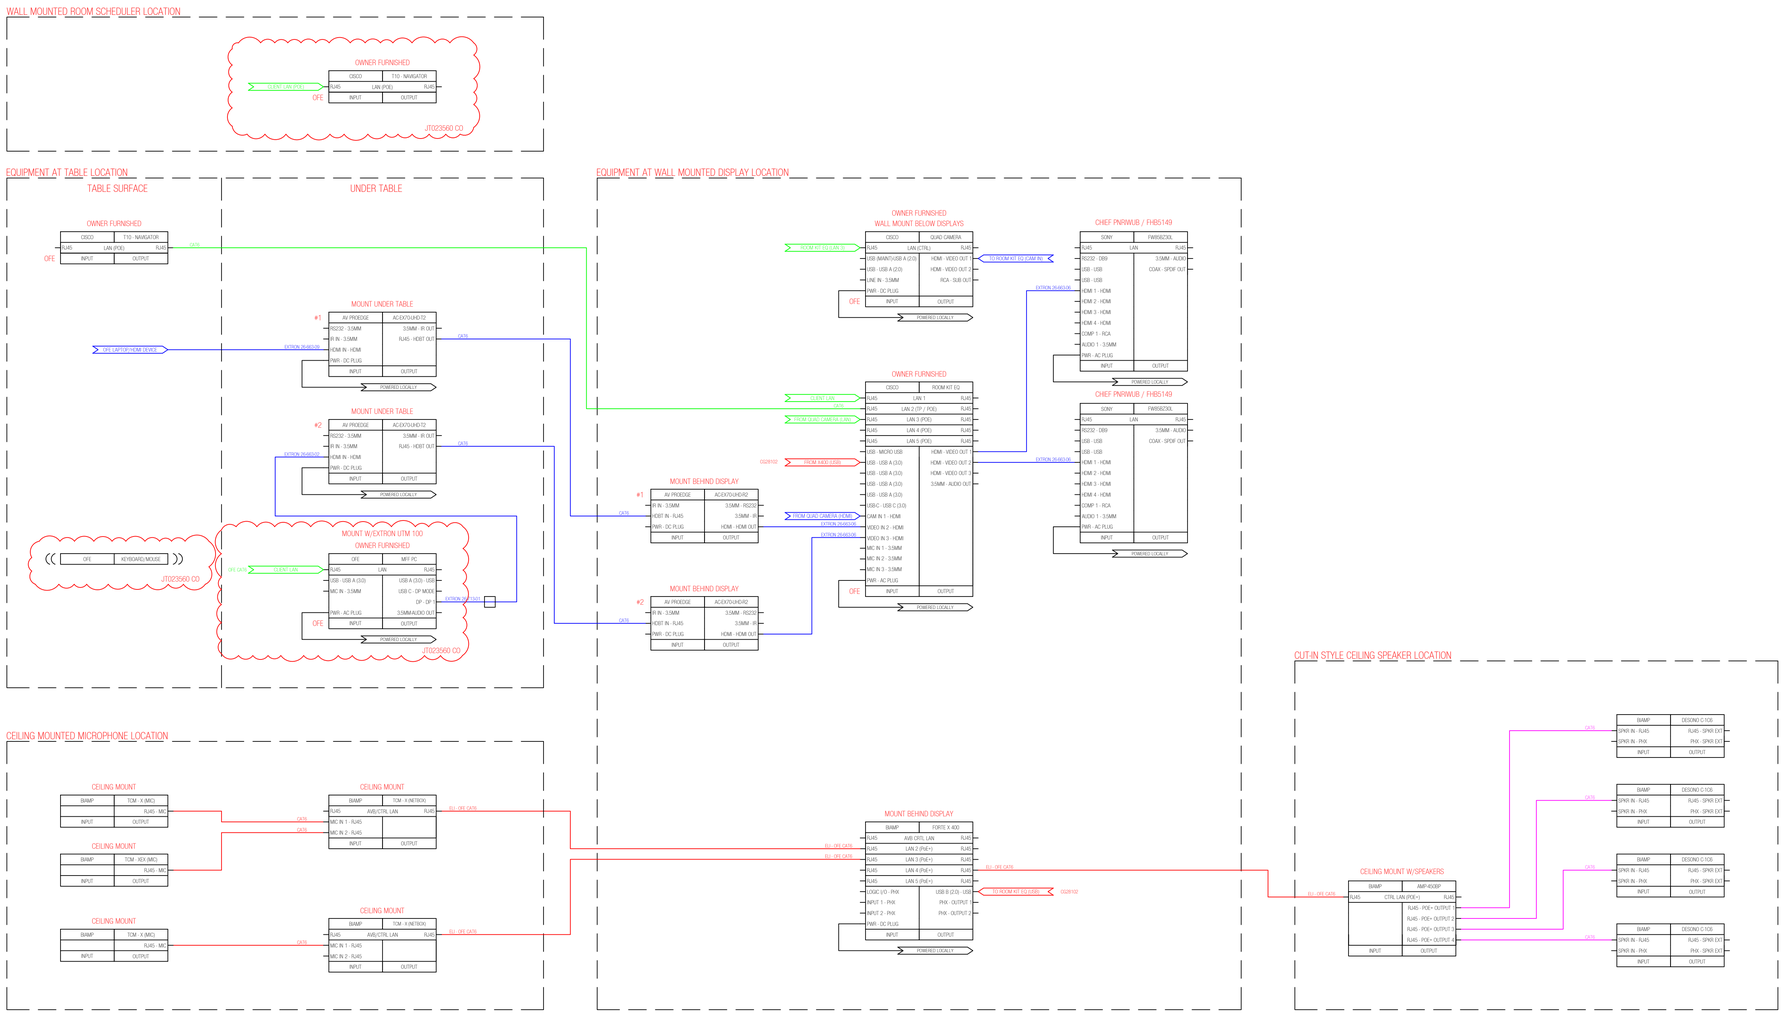

LEAD TECHNICIAN (PRINT): _____

NETWORK REQUIREMENTS			POWER REQUIREMENTS		
QTY	DEVICE	LOCATION	QTY	CIRCUIT/SIZE	LOCATION
1	ROOMKIT EQ	DISPLAY LOCATION	1	15A QUAD	DISPLAY LOCATION
1	ROOM SCHEDULER	OUTSIDE ROOM	1	15A QUAD	TABLE LOCATION
1	OFE PC	FLOOR (CONF. TABLE)	-	-	-
-	-	-	-	-	-
-	-	-	-	-	-
-	-	-	-	-	-
-	-	-	-	-	-
-	-	-	-	-	-
-	-	-	-	-	-
-	-	-	-	-	-
-	-	-	-	-	-

CLIENT NAME: LOCKTON DUNNING

REV:	DATE:	DRAWN BY:
0	03/05/2026	AFS
		-

TAURUS technologies
1420 LAKESIDE PARKWAY, SUITE 100, FLOWER MOUND, TX 75028
WWW.TAURUSTECHINC.COM 1-888-410-5747

ROOM NAME: VICTORY COMMONS - 15TH FLOOR - ELEVATED CONF ROOM 15.104

SITE ADDRESS: 2601 VICTORY AVE, DALLAS, TX 75219

PROJECT NO: JT022715, JT023560, JT023785, JT023822, JT023861 & JT023995

SHEET SIZE:	SCALE:	SHEET NO:
24 X 36	1 : 1	TA-719

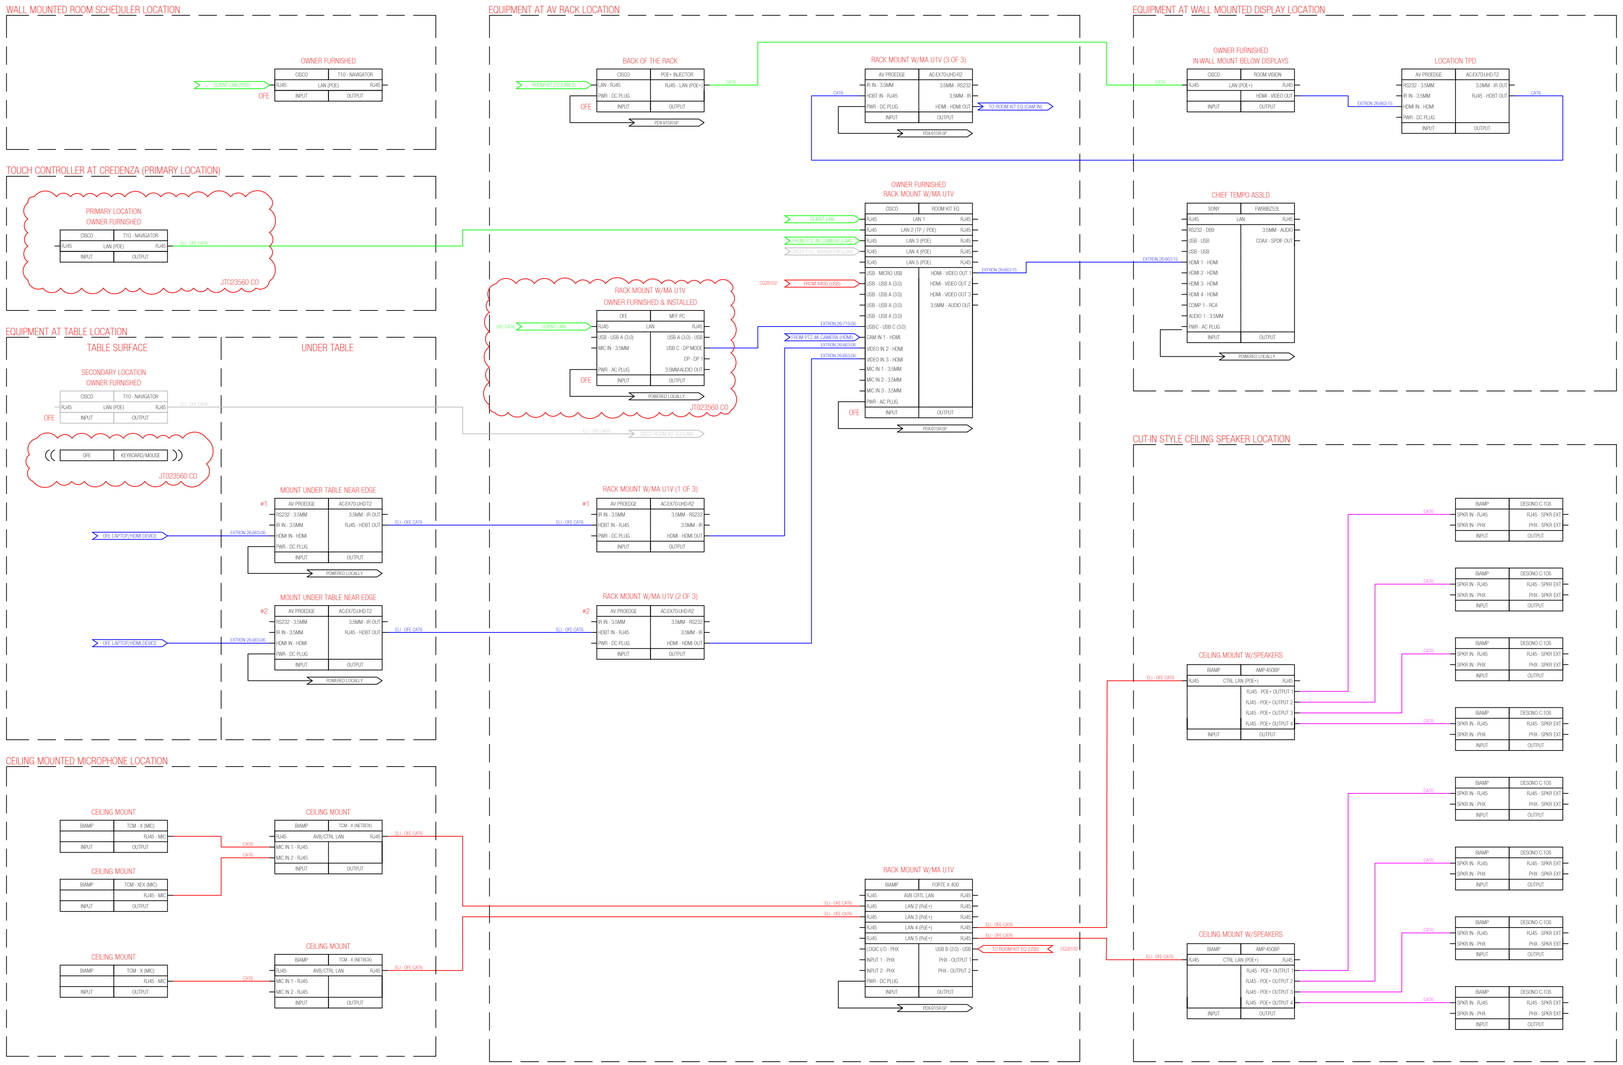

LEAD TECH NOTE: MIDDLE ATLANTIC RACK FAN (CO JT023822)

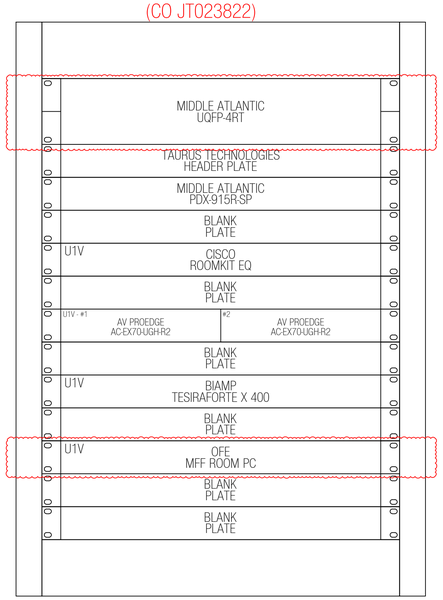

NETWORK REQUIREMENTS		
QTY	DEVICE	LOCATION
1	ROOMKIT EQ	RACK LOCATION
1	ROOM SCHEDULER	OUTSIDE ROOM
1	OFE PC	RACK LOCATION
-	-	-
-	-	-
-	-	-
-	-	-
-	-	-
-	-	-
-	-	-
-	-	-

POWER REQUIREMENTS		
QTY	CIRCUIT/SIZE	LOCATION
1	15A DUPLEX	DISPLAY LOCATION
1	15A DUPLEX	TABLE LOCATION
1	15A DUPLEX	RACK LOCATION
-	-	-
-	-	-
-	-	-
-	-	-
-	-	-
-	-	-
-	-	-
-	-	-

CLIENT NAME:

LOCKTON DUNNING

REV:	DATE:	DRAWN BY:
0	03/05/2026	AFS
-	-	-
-	-	-
-	-	-
-	-	-
-	-	-
-	-	-
-	-	-
-	-	-

TAURUS technologies
1420 LAKESIDE PARKWAY, SUITE 100, FLOWER MOUND, TX 75028
WWW.TAURUSTECHINC.COM 1-888-410-5747

LEAD TECHNICIAN (PRINT): _____

ROOM NAME: VICTORY COMMONS - 15TH FLOOR - LARGE CONF ROOM 15.076

SITE ADDRESS: 2601 VICTORY AVE, DALLAS, TX 75219

PROJECT NO: JT022715, JT023560, JT023785, JT023822, JT023861 & JT023995

SHEET SIZE:	SCALE:	SHEET NO:
24 X 36	1 : 1	TA-720

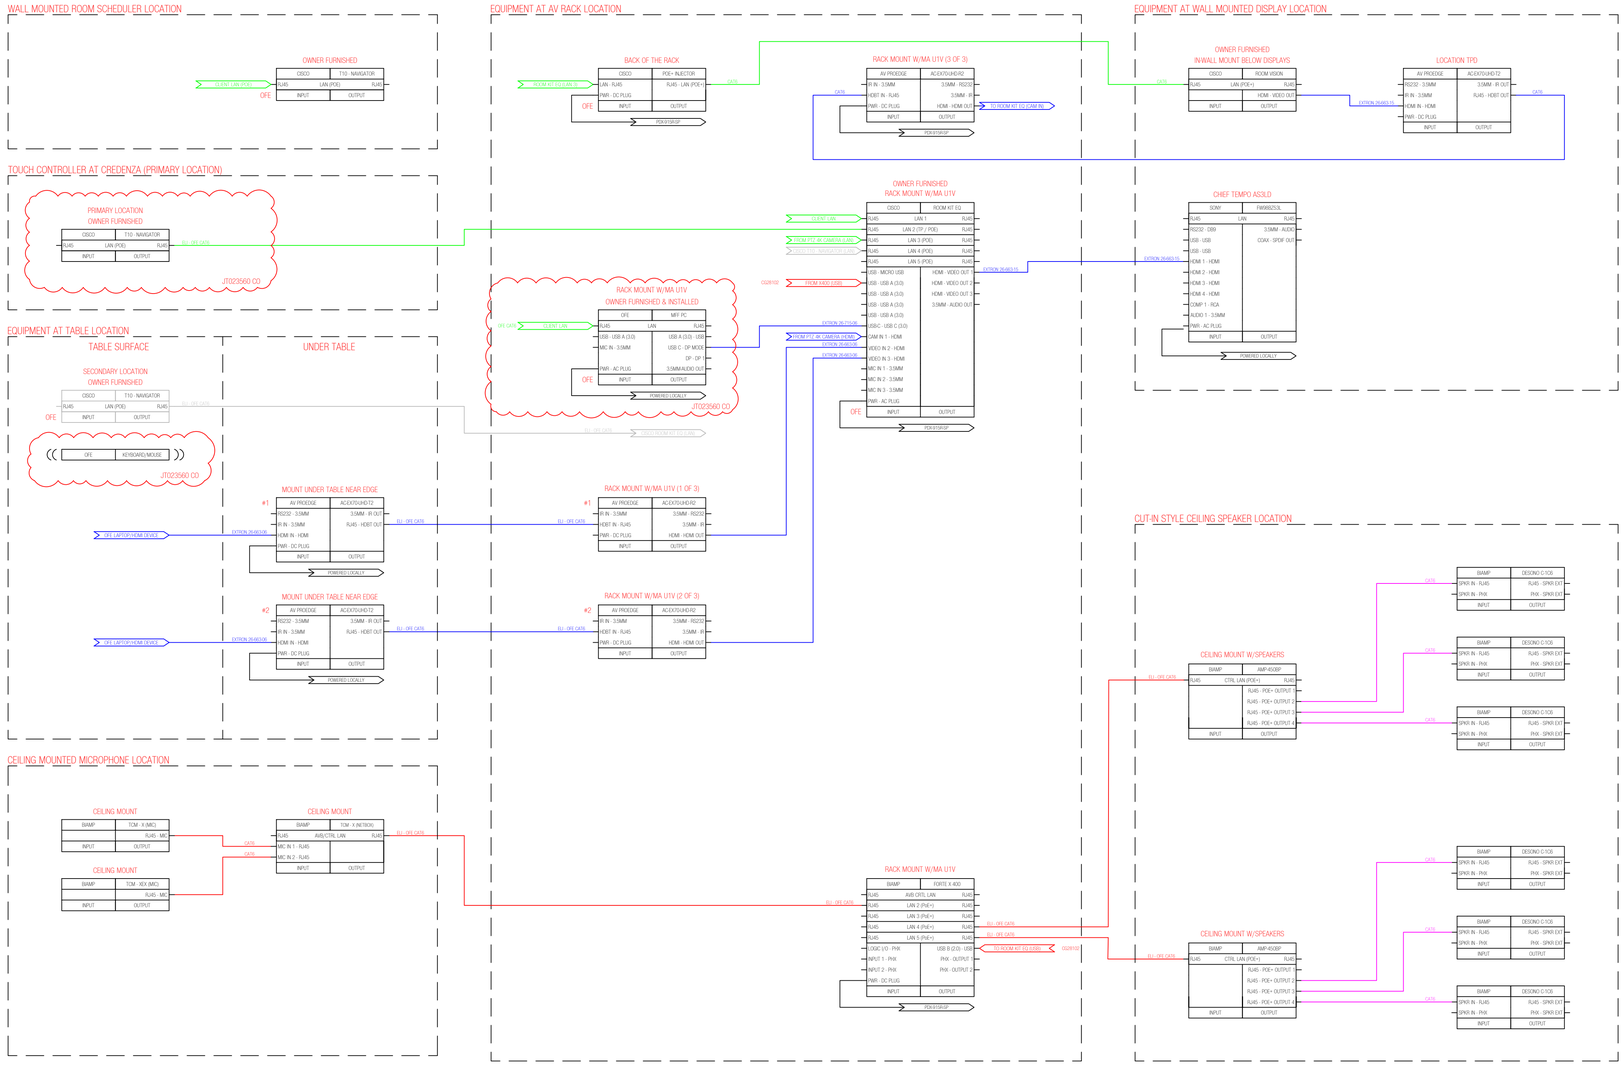

LEAD TECH NOTE: MIDDLE ATLANTIC RACK FAN (CO JT023822)

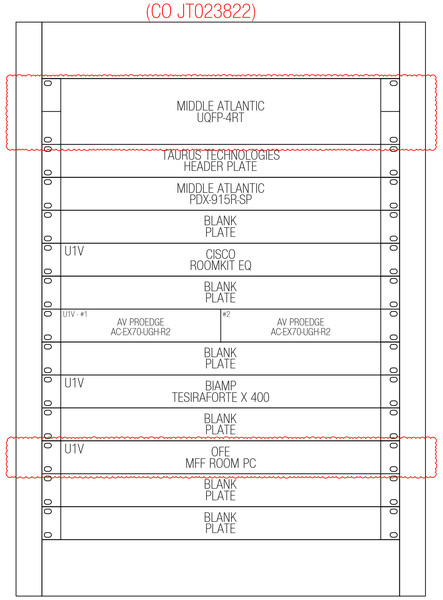

NETWORK REQUIREMENTS		
QTY	DEVICE	LOCATION
1	ROOMKIT EQ	RACK LOCATION
1	ROOM SCHEDULER	OUTSIDE ROOM
1	OFE PC	RACK LOCATION
-	-	-
-	-	-
-	-	-
-	-	-
-	-	-
-	-	-
-	-	-
-	-	-

POWER REQUIREMENTS		
QTY	CIRCUIT/SIZE	LOCATION
1	15A DUPLEX	DISPLAY LOCATION
1	15A DUPLEX	TABLE LOCATION
1	15A DUPLEX	RACK LOCATION
-	-	-
-	-	-
-	-	-
-	-	-
-	-	-
-	-	-
-	-	-
-	-	-

CLIENT NAME: LOCKTON DUNNING

REV:	DATE:	DRAWN BY:
0	03/05/2026	AFS

TAURUS technologies
1420 LAKESIDE PARKWAY, SUITE 100, FLOWER MOUND, TX 75028
WWW.TAURUSTECHNIC.COM 1-888-410-5747

LEAD TECHNICIAN (PRINT): _____

ROOM NAME: VICTORY COMMONS - 15TH FLOOR - LARGE CONF ROOM 15.077

SITE ADDRESS: 2601 VICTORY AVE, DALLAS, TX 75219

PROJECT NO: JT022715, JT023560, JT023785, JT023822, JT023861 & JT023995

SHEET SIZE:	SCALE:	SHEET NO:
24 X 36	1 : 1	TA-721

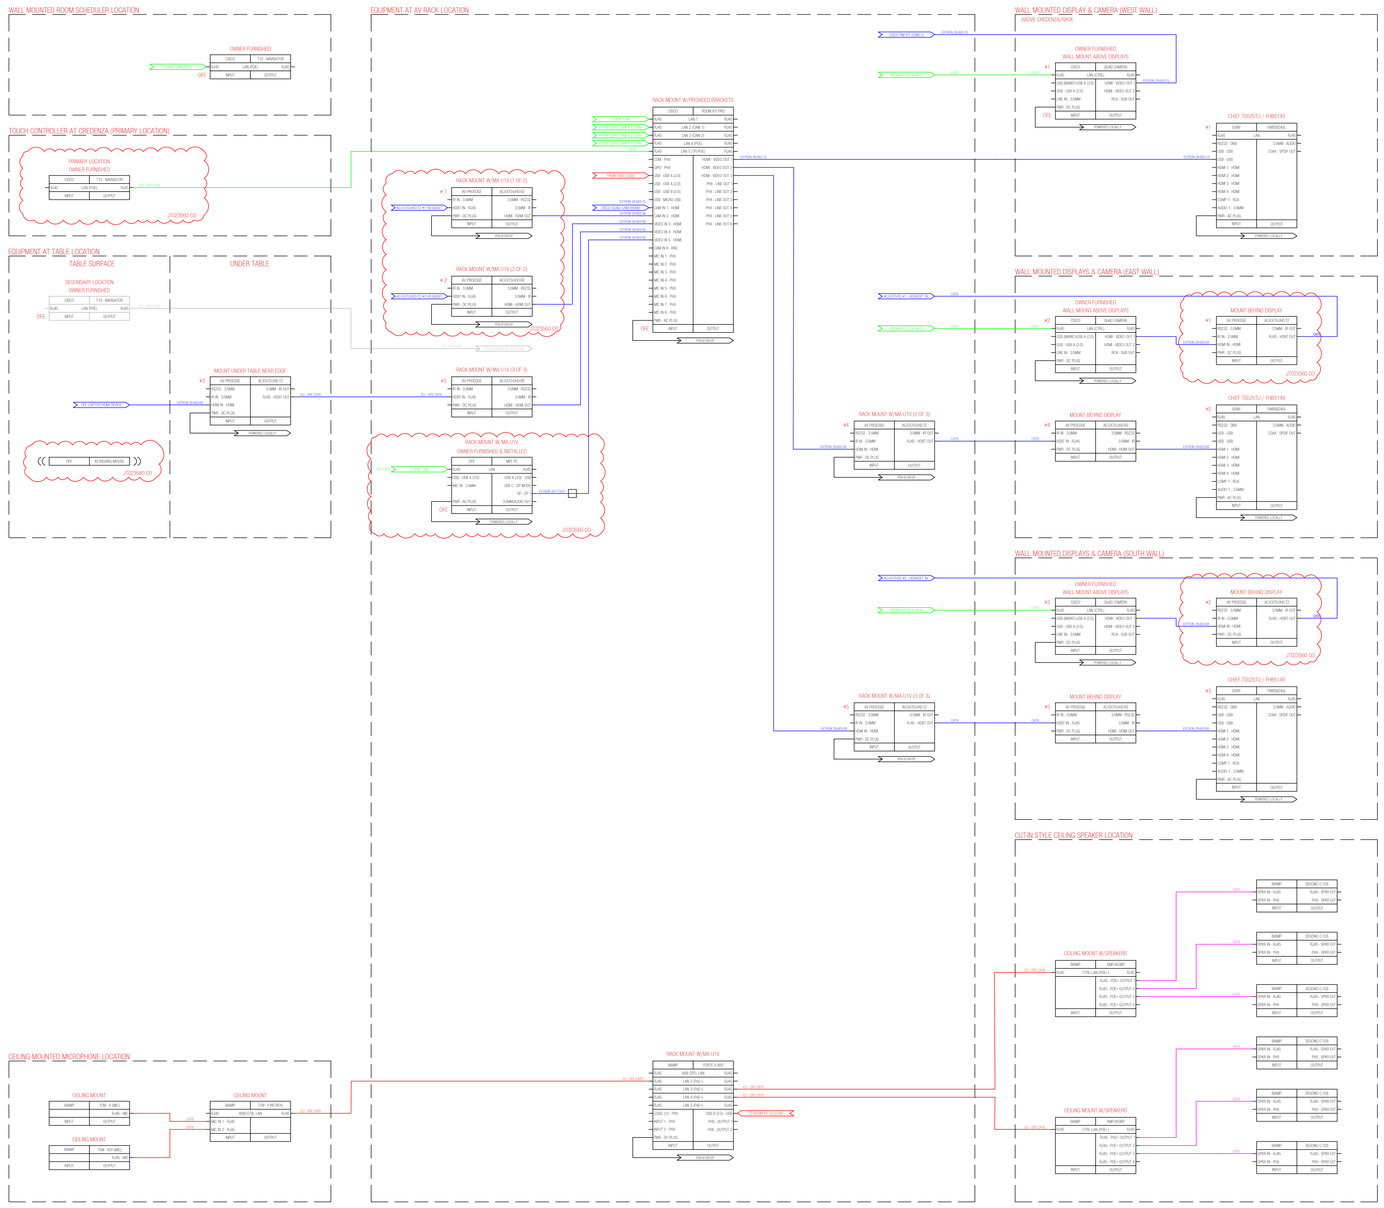

LEAD TECH NOTE: MIDDLE ATLANTIC RACK FAN (CO JT023822)

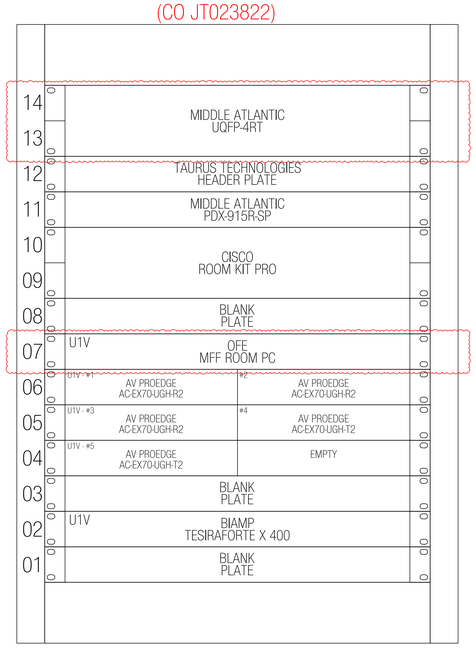

NETWORK REQUIREMENTS			POWER REQUIREMENTS		
QTY:	DEVICE	LOCATION	QTY:	CIRCUIT/SIZE	LOCATION
1	ROOMKIT EQ	RACK LOCATION	1	15A DUPLEX	EACH DISPLAY LOCATION
1	ROOM SCHEDULER	OUTSIDE ROOM	1	15A DUPLEX	TABLE LOCATION
1	OFE PC	RACK LOCATION	1	15A DUPLEX	RACK LOCATION
-	-	-	-	-	-
-	-	-	-	-	-
-	-	-	-	-	-
-	-	-	-	-	-
-	-	-	-	-	-
-	-	-	-	-	-
-	-	-	-	-	-
-	-	-	-	-	-
-	-	-	-	-	-
-	-	-	-	-	-

CLIENT NAME: LOCKTON DUNNING

REV:	DATE:	DRAWN BY:
0	03/05/2026	AFS

TAURUS Technologies
1420 LAKESIDE PARKWAY, SUITE 100, FLOWER MOUND, TX 75028
WWW.TAURUSTECHINC.COM T-888-410-5747

LEAD TECHNICIAN (PRINT): _____

ROOM NAME: VICTORY COMMONS - 15TH FLOOR - LARGE CONF ROOM 15.078

SITE ADDRESS: 2601 VICTORY AVE, DALLAS, TX 75219

PROJECT NO: JT022715, JT023560, JT023785, JT023822, JT023861 & JT023995

SHEET SIZE:	SCALE:	SHEET NO:
36 X 48	1 : 1	TA-722

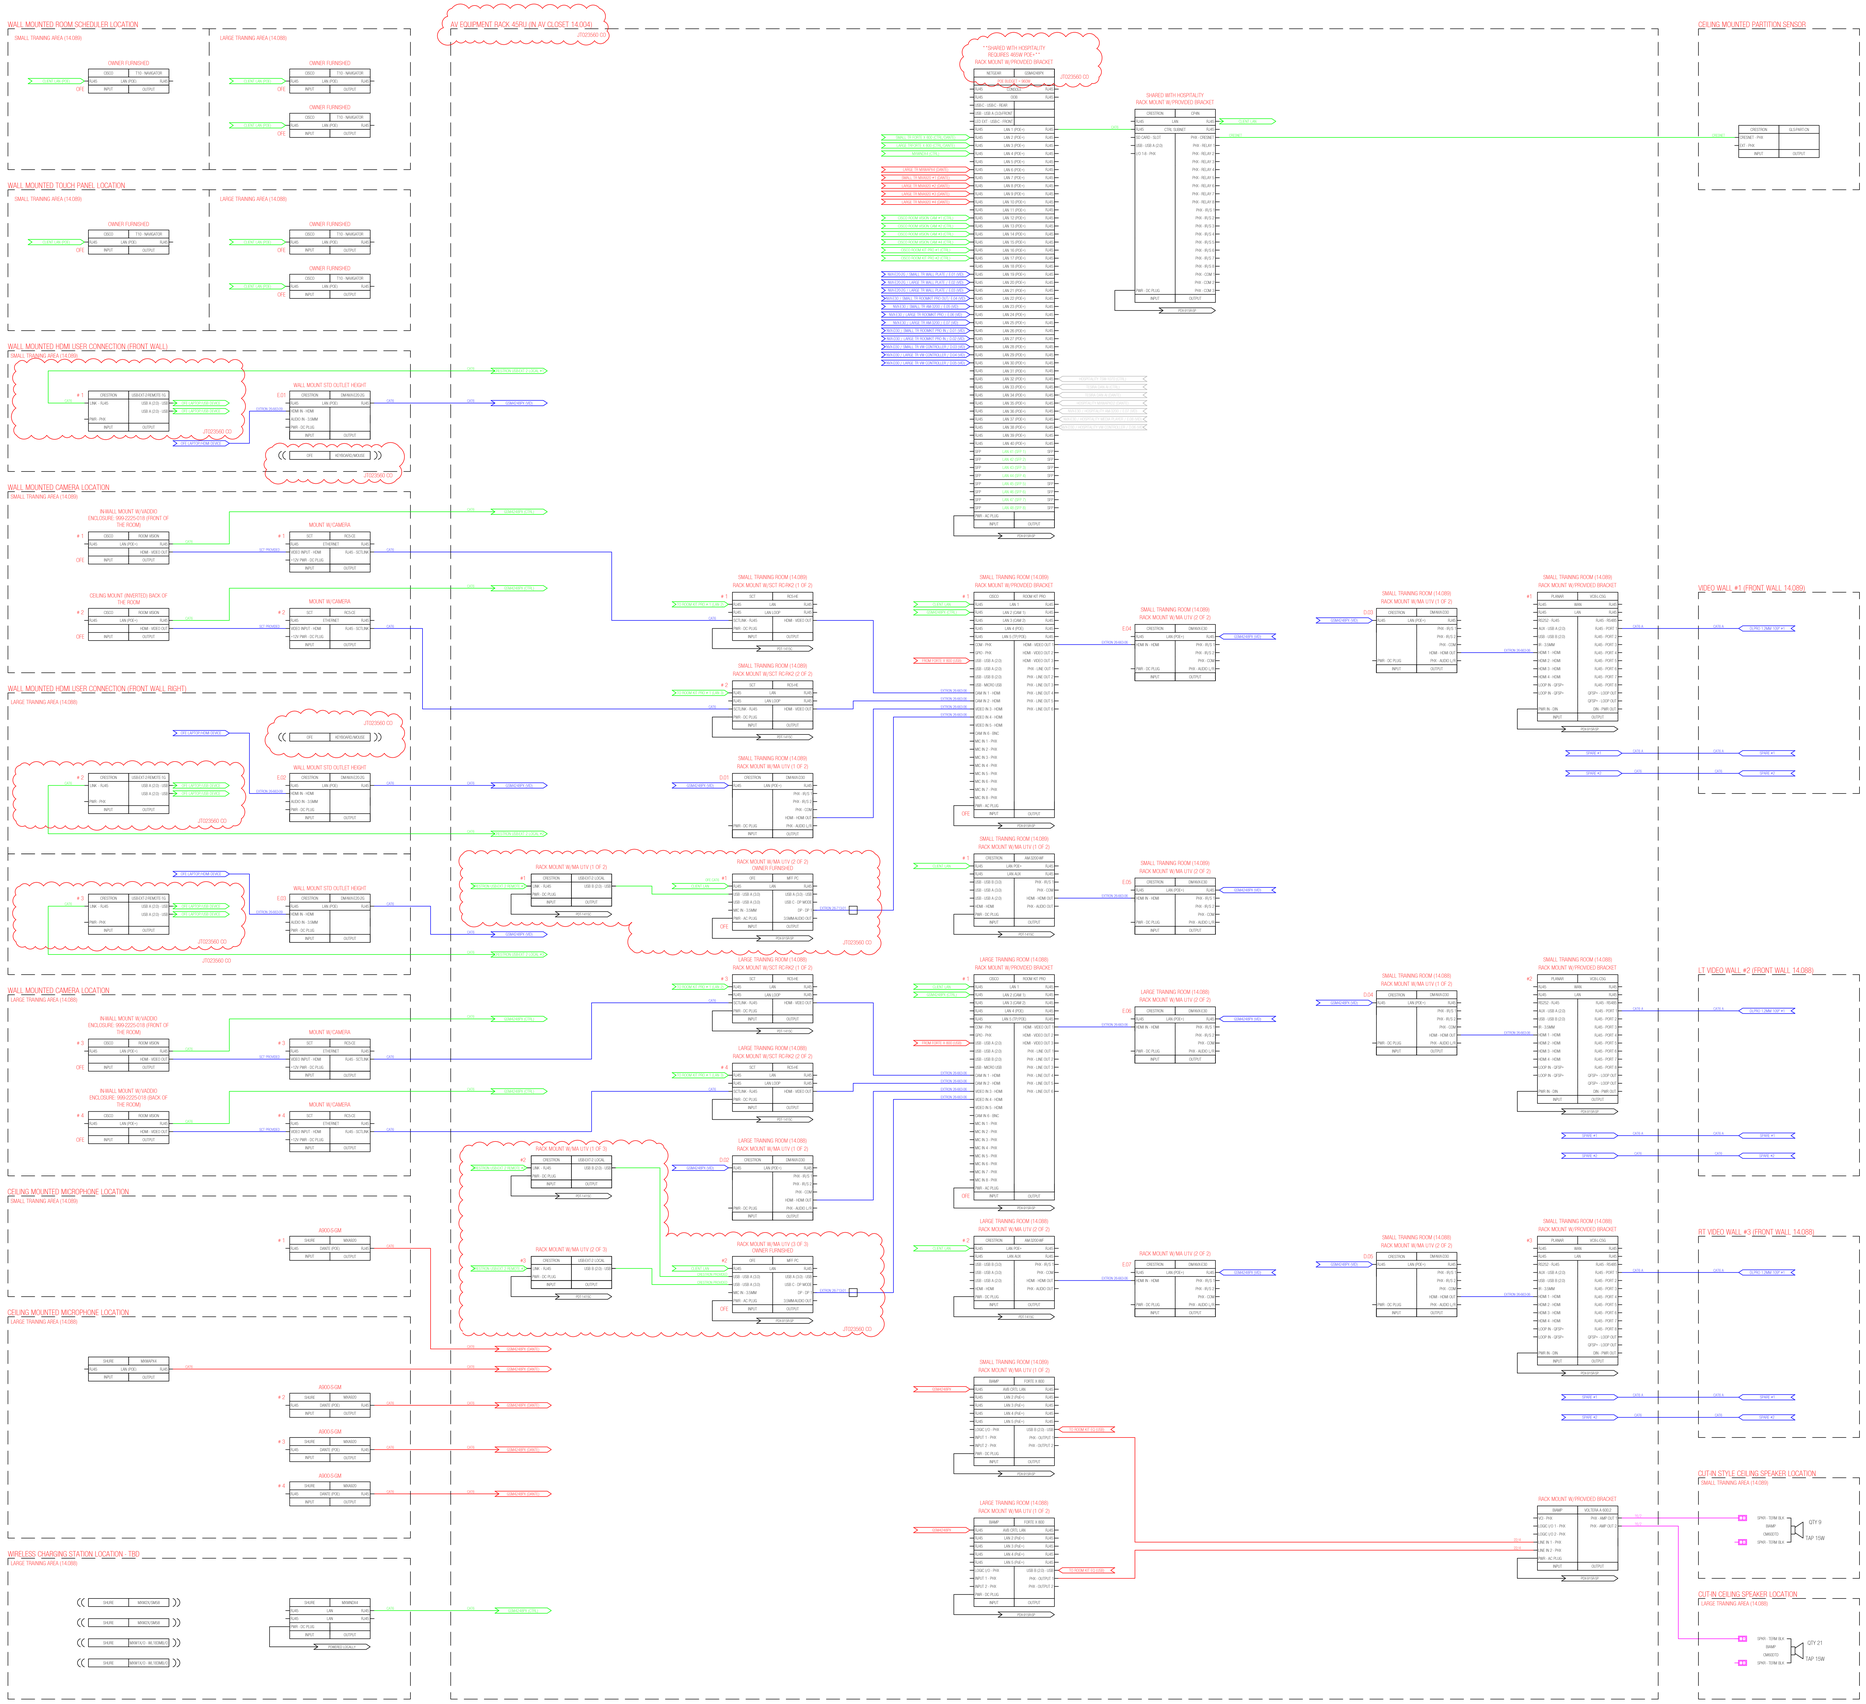

IDF RACK 14.004
TRAINING ROOM / HOSPITALITY
SEE TA-730

NETWORK REQUIREMENTS			NETWORK REQUIREMENTS			POWER REQUIREMENTS		
QTY	DEVICE	LOCATION	QTY	DEVICE	LOCATION	QTY	CIRCUIT/SIZE	LOCATION
2	ROOMKIT PRO	RACK LOCATION	1	CRE PC #1	AV RACK	4	15A DUPLEX	EACH VIDEO WALL LOCATION
1	CP4N	RACK LOCATION	1	CRE PC #2	AV RACK	1	15A DUPLEX	TABLE LOCATION
2	AIR MEDIA	RACK LOCATION	-	-	-	4	15A DUPLEX	RACK LOCATION
1 POE	ROOM SCHEDULER	SMALL TR.	-	-	-	5	15A DUPLEX	CHARGER TBD LOCATION
1	NAVIGATOR	SMALL TR.	-	-	-	-	-	-
2 POE	ROOM SCHEDULER	LARGE TR.	-	-	-	-	-	-
2	NAVIGATOR	LARGE TR.	-	-	-	-	-	-
1	AIR MEDIA	RACK LOCATION	-	-	-	-	-	-
2	SONOS PORT	RACK LOCATION	-	-	-	-	-	-
1	MEDIA PLAYER	RACK LOCATION	-	-	-	-	-	-

CLIENT NAME:
LOCKTON DUNNING

TAURUS technologies
1420 LAKESIDE PARKWAY, SUITE 100, FLOWER MOUND, TX 75028
WWW.TAURUSTECHINC.COM T-888-410-5747

LEAD TECHNICIAN (PRINT):	
ROOM NAME:	VICTORY COMMONS - 14TH FLOOR - DIVISIBLE TRAINING RM 14.089
SITE ADDRESS:	2601 VICTORY AVE, DALLAS, TX 75219
PROJECT NO:	JT022715, JT023560, JT023785, JT023822, JT023861 & JT023995

REV:	DATE:	DRAWN BY:
0	03/05/2026	AFS

SHEET SIZE:	SCALE:	SHEET NO:
36 X 48	1 : 1	TA-723

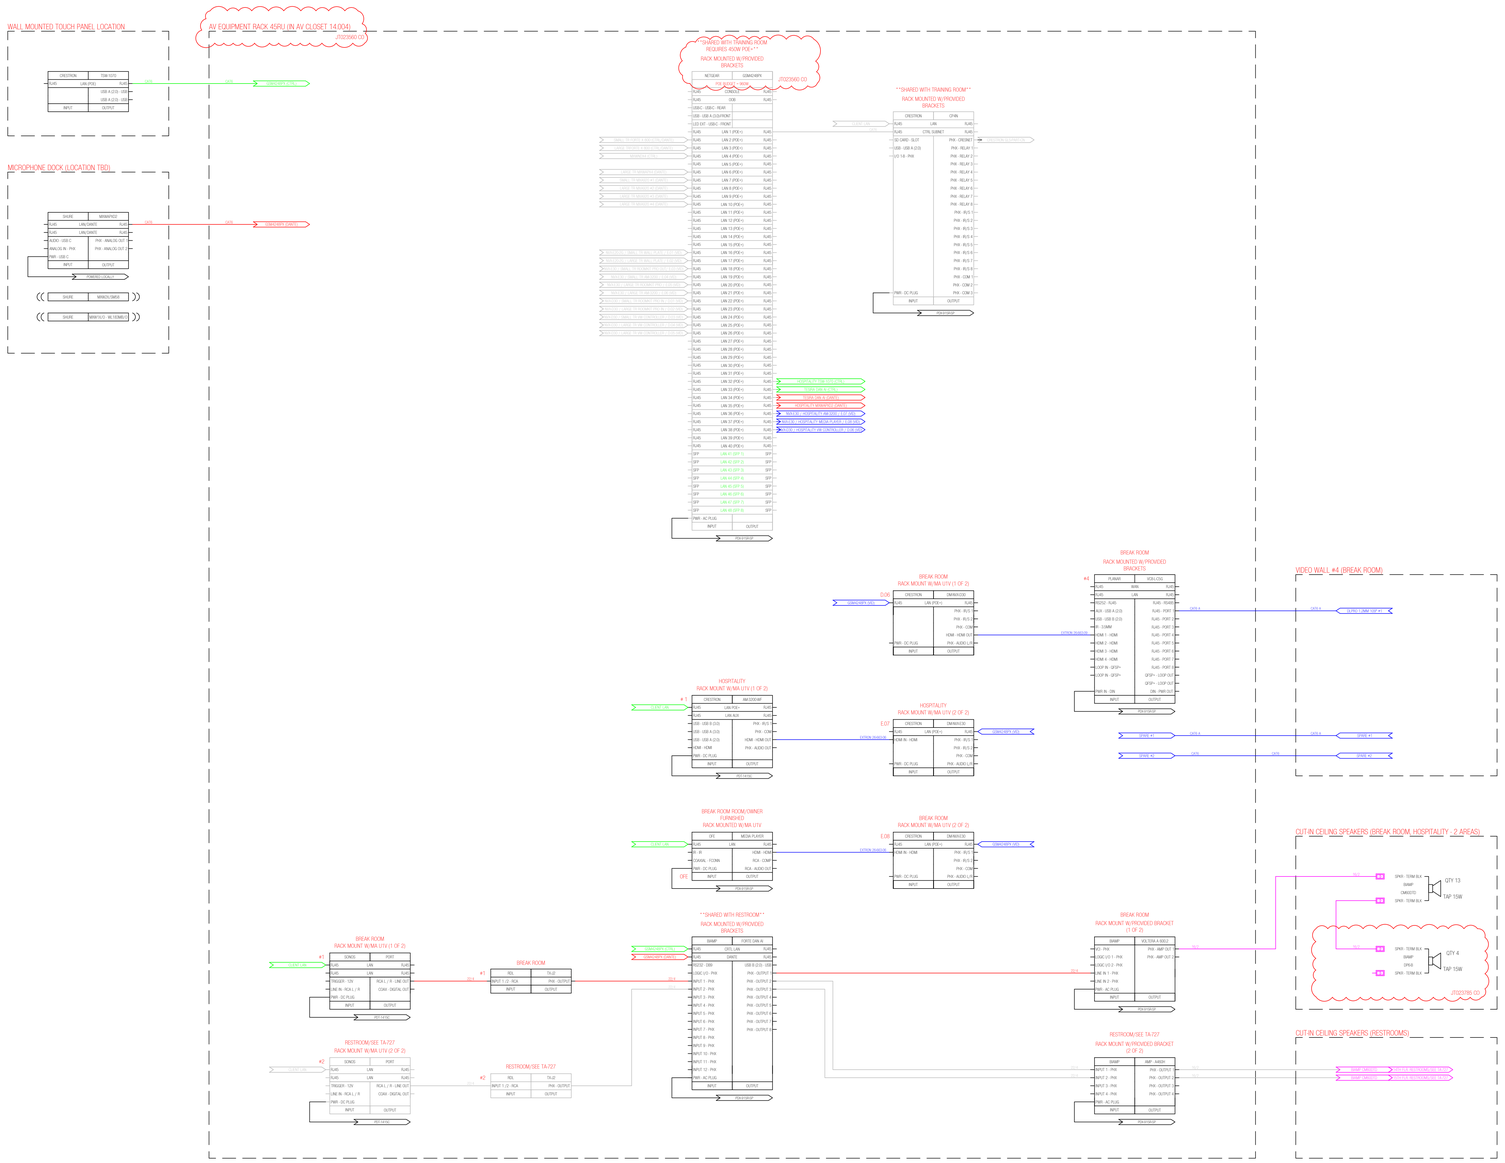
WALL MOUNTED TOUCH PANEL LOCATION
CRESTRON
TSW-1070
RJ45
LAN (POE)
USB-B (CS)
USB-A (CS)
INPUT
OUTPUT
CAT6
CAT6 | CATV | CTS
MICROPHONE DOCK (LOCATION TBD)
SHURE
MXWANI2
LAN/LINK1
LAN/LINK2
ANALOG IN - PHX
ANALOG OUT 1
ANALOG OUT 2
PWR - USB C
INPUT
OUTPUT
AUX
CAT6 | AUX
CONTROL | CAT6
SHURE
MXWCS-TMPW
SHURE
MXWFXLO - WL FIXEDMLO
AV EQUIPMENT RACK 45RU IN AV CLOSET 14.004
JT023560 C2
**SHARED WITH TRAINING ROOM
REQUIRES 450W VIA **
RACK MOUNTED W/ PROVIDED
BRACKETS
NETGEAR
GS348MXPS
JT023560 C2
SHARED WITH TRAINING ROOM
RACK MOUNTED W/ PROVIDED
BRACKETS
CRESTRON
CP4N
CTN_SUBNET
SD CARD - SLOT
USB - USB A (CS)
I/O 16 - PHX
PHX - CRESTNET
PHX - RELAY 1
PHX - RELAY 2
PHX - RELAY 3
PHX - RELAY 4
PHX - RELAY 5
PHX - RELAY 6
PHX - RELAY 7
PHX - RELAY 8
PHX - R/S 1
PHX - R/S 2
PHX - R/S 3
PHX - R/S 4
PHX - R/S 5
PHX - R/S 6
PHX - R/S 7
PHX - R/S 8
PHX - COM 1
PHX - COM 2
PHX - COM 3
PWR - DC PLUG
INPUT
OUTPUT
PWR CONDIT
LAN 1 (POE +)
LAN 2 (POE +)
LAN 3 (POE +)
LAN 4 (POE +)
LAN 5 (POE +)
LAN 6 (POE +)
LAN 7 (POE +)
LAN 8 (POE +)
LAN 9 (POE +)
LAN 10 (POE +)
LAN 11 (POE +)
LAN 12 (POE +)
LAN 13 (POE +)
LAN 14 (POE +)
LAN 15 (POE +)
LAN 16 (POE +)
LAN 17 (POE +)
LAN 18 (POE +)
LAN 19 (POE +)
LAN 20 (POE +)
LAN 21 (POE +)
LAN 22 (POE +)
LAN 23 (POE +)
LAN 24 (POE +)
LAN 25 (POE +)
LAN 26 (POE +)
LAN 27 (POE +)
LAN 28 (POE +)
LAN 29 (POE +)
LAN 30 (POE +)
LAN 31 (POE +)
LAN 32 (POE +)
LAN 33 (POE +)
LAN 34 (POE +)
LAN 35 (POE +)
LAN 36 (POE +)
LAN 37 (POE +)
LAN 38 (POE +)
LAN 39 (POE +)
LAN 40 (POE +)
LAN 41 (SFP 1)
LAN 42 (SFP 2)
LAN 43 (SFP 3)
LAN 44 (SFP 4)
LAN 45 (SFP 5)
LAN 46 (SFP 6)
LAN 47 (SFP 7)
LAN 48 (SFP 8)
PWR - AC PLUG
INPUT
OUTPUT
PWR CONDIT
CAT6 | CATV | CTS
CAT6 | CATV | CTS
CAT6 | CATV | CTS

EQUIPMENT AT WALL MOUNTED DISPLAY LOCATION

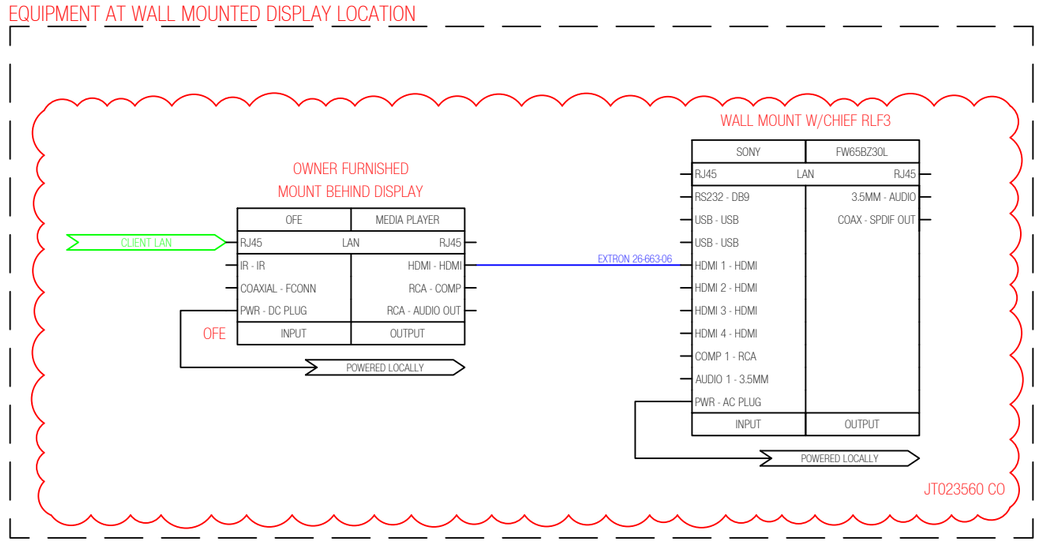

LEAD TECHNICIAN (PRINT): _____

NETWORK REQUIREMENTS			POWER REQUIREMENTS		
QTY	DEVICE	LOCATION	QTY	CIRCUIT/SIZE	LOCATION
1	MEDIA PLAYER	DISPLAY LOCATION	1	15A DUPLEX	DISPLAY LOCATION
-	-	-	-	-	-
-	-	-	-	-	-
-	-	-	-	-	-
-	-	-	-	-	-
-	-	-	-	-	-
-	-	-	-	-	-
-	-	-	-	-	-
-	-	-	-	-	-
-	-	-	-	-	-

CLIENT NAME:

LOCKTON DUNNING

REV:	DATE:	DRAWN BY:
0	03/05/2026	AFS
-	-	-

TAURUS technologies
1420 LAKESIDE PARKWAY, SUITE 100, FLOWER MOUND, TX 75028
WWW.TAURUSTECHINC.COM 1-888-410-5747

ROOM NAME: VICTORY COMMONS - 15TH FLOOR - RECEPTION 14.001

SITE ADDRESS: 2601 VICTORY AVE, DALLAS, TX 75219

PROJECT NO: JT022715, JT023560, JT023785, JT023822, JT023861 & JT023995

SHEET SIZE:	SCALE:	SHEET NO:
11 X 17	1 : 1	TA-725

EQUIPMENT AT WALL MOUNTED DISPLAY LOCATION

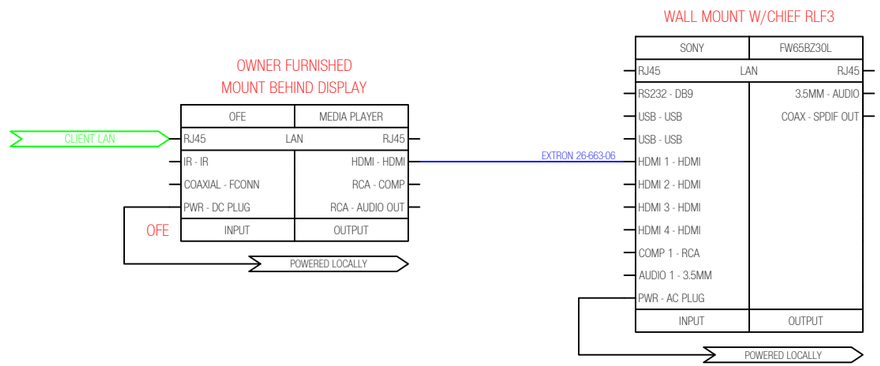

LEAD TECHNICIAN (PRINT): _____

NETWORK REQUIREMENTS			POWER REQUIREMENTS		
QTY	DEVICE	LOCATION	QTY	CIRCUIT/SIZE	LOCATION
1	MEDIA PLAYER	DISPLAY LOCATION	1	15A DUPLEX	DISPLAY LOCATION
-	-	-	-	-	-
-	-	-	-	-	-
-	-	-	-	-	-
-	-	-	-	-	-
-	-	-	-	-	-
-	-	-	-	-	-
-	-	-	-	-	-
-	-	-	-	-	-
-	-	-	-	-	-

CLIENT NAME:

LOCKTON DUNNING

REV:	DATE:	DRAWN BY:
0	03/05/2026	AFS
-	-	-

TAURUS technologies
1420 LAKESIDE PARKWAY, SUITE 100, FLOWER MOUND, TX 75028
WWW.TAURUSTECHINC.COM 1-888-410-5747

ROOM NAME: VICTORY COMMONS - 15TH FLOOR - RECEPTION 15.001

SITE ADDRESS: 2601 VICTORY AVE, DALLAS, TX 75219

PROJECT NO: JT022715, JT023560, JT023785, JT023822, JT023861 & JT023995

SHEET SIZE:	SCALE:	SHEET NO:
11 X 17	1 : 1	TA-726

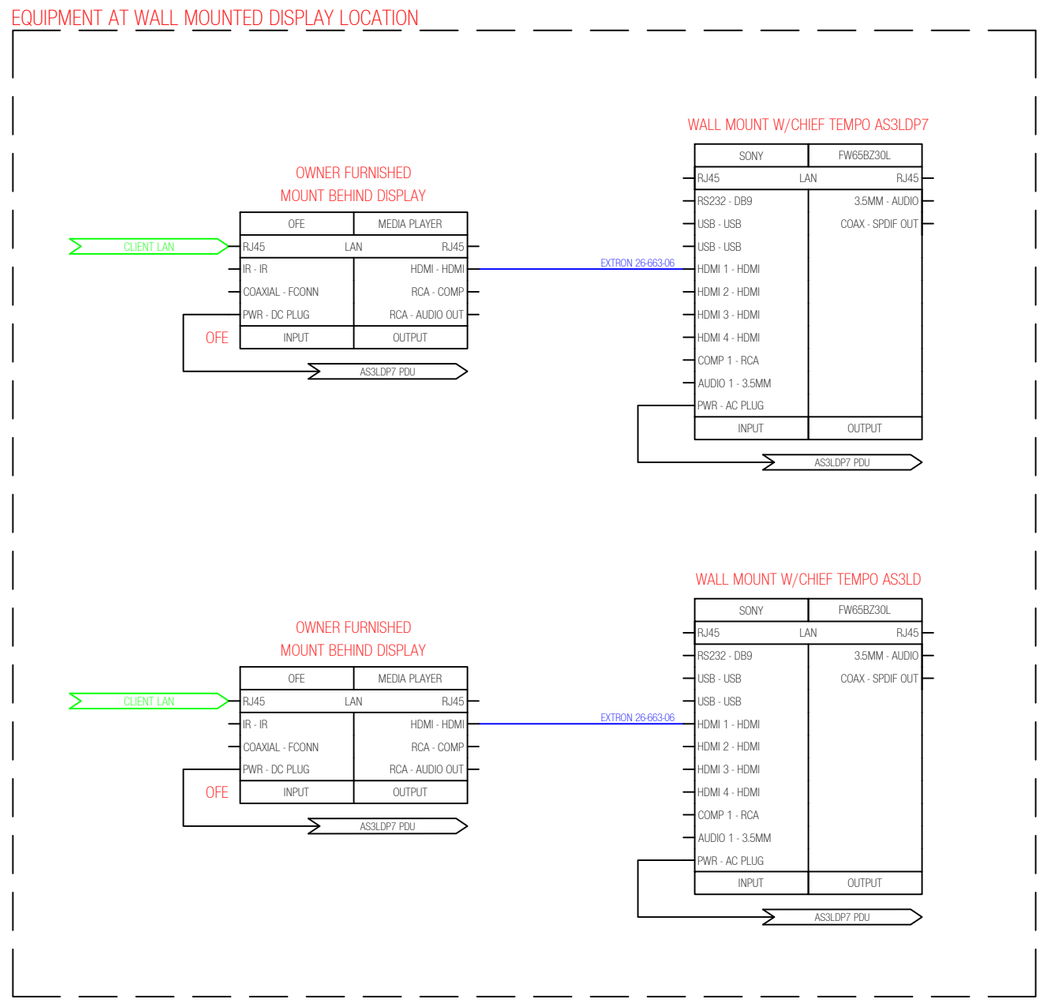

LEAD TECHNICIAN (PRINT): _____

NETWORK REQUIREMENTS			POWER REQUIREMENTS		
QTY	DEVICE	LOCATION	QTY	CIRCUIT/SIZE	LOCATION
1	MEDIA PLAYER	EACH DISPLAY LOCATION	1	15A DUPLEX	EACH DISPLAY LOCATION
-	-	-	-	-	-
-	-	-	-	-	-
-	-	-	-	-	-
-	-	-	-	-	-
-	-	-	-	-	-
-	-	-	-	-	-
-	-	-	-	-	-
-	-	-	-	-	-
-	-	-	-	-	-

CLIENT NAME:

LOCKTON DUNNING

REV:	DATE:	DRAWN BY:
0	03/05/2026	AFS
-	-	-

TAURUS technologies
1420 LAKESIDE PARKWAY, SUITE 100, FLOWER MOUND, TX 75028
WWW.TAURUSTECHINC.COM 1-888-410-5747

ROOM NAME: VICTORY COMMONS - 15TH FLOOR - COLLAB 15.028

SITE ADDRESS: 2601 VICTORY AVE, DALLAS, TX 75219

PROJECT NO: JT022715, JT023560, JT023785, JT023822, JT023861 & JT023995

SHEET SIZE:	SCALE:	SHEET NO:
11 X 17	1 : 1	TA-727

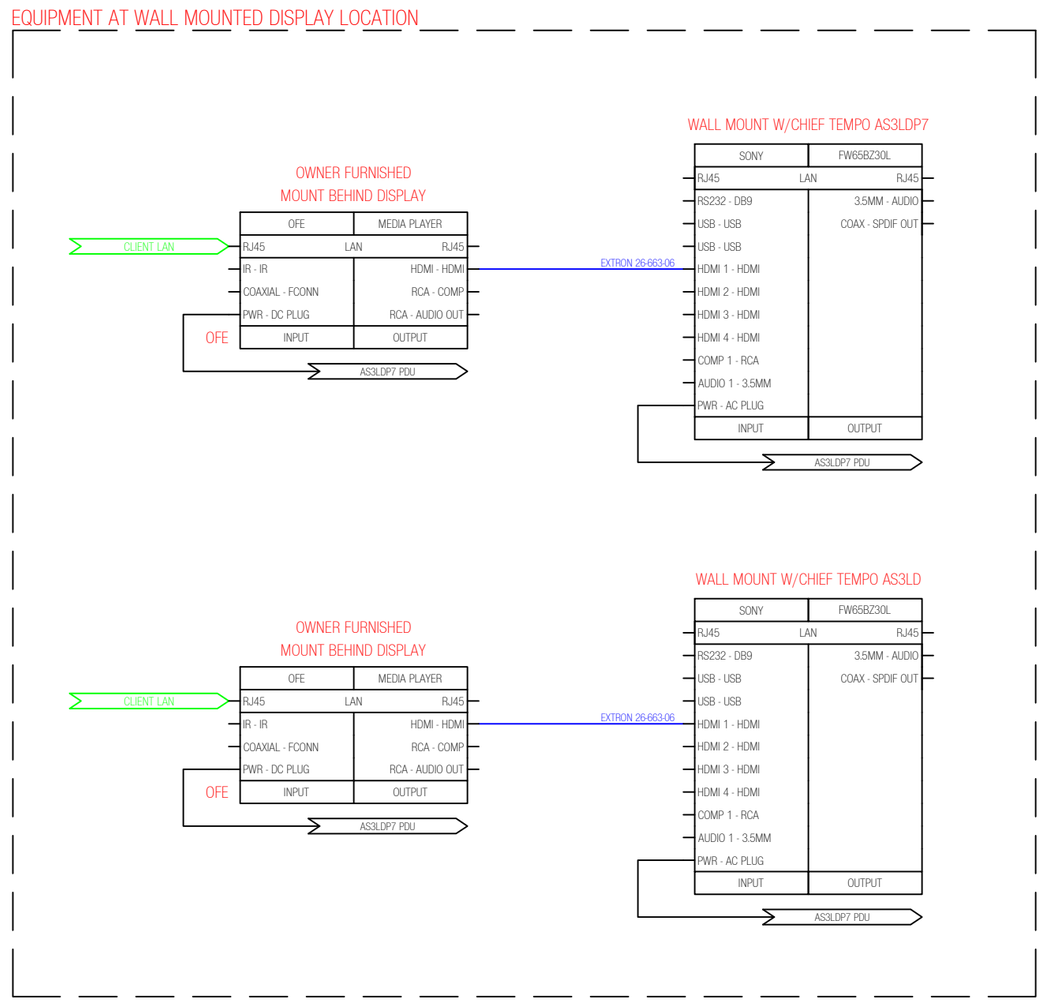

LEAD TECHNICIAN (PRINT): _____

NETWORK REQUIREMENTS			POWER REQUIREMENTS		
QTY	DEVICE	LOCATION	QTY	CIRCUIT/SIZE	LOCATION
1	MEDIA PLAYER	EACH DISPLAY LOCATION	1	15A DUPLEX	EACH DISPLAY LOCATION
-	-	-	-	-	-
-	-	-	-	-	-
-	-	-	-	-	-
-	-	-	-	-	-
-	-	-	-	-	-
-	-	-	-	-	-
-	-	-	-	-	-
-	-	-	-	-	-
-	-	-	-	-	-

CLIENT NAME:

LOCKTON DUNNING

REV:	DATE:	DRAWN BY:
0	03/05/2026	AFS
-	-	-

TAURUS technologies
1420 LAKESIDE PARKWAY, SUITE 100, FLOWER MOUND, TX 75028
WWW.TAURUSTECHINC.COM 1-888-410-5747

ROOM NAME: VICTORY COMMONS - 15TH FLOOR - COLLAB 15.049

SITE ADDRESS: 2601 VICTORY AVE, DALLAS, TX 75219

PROJECT NO: JT022715, JT023560, JT023785, JT023822, JT023861 & JT023995

SHEET SIZE:	SCALE:	SHEET NO:
11 X 17	1 : 1	TA-728

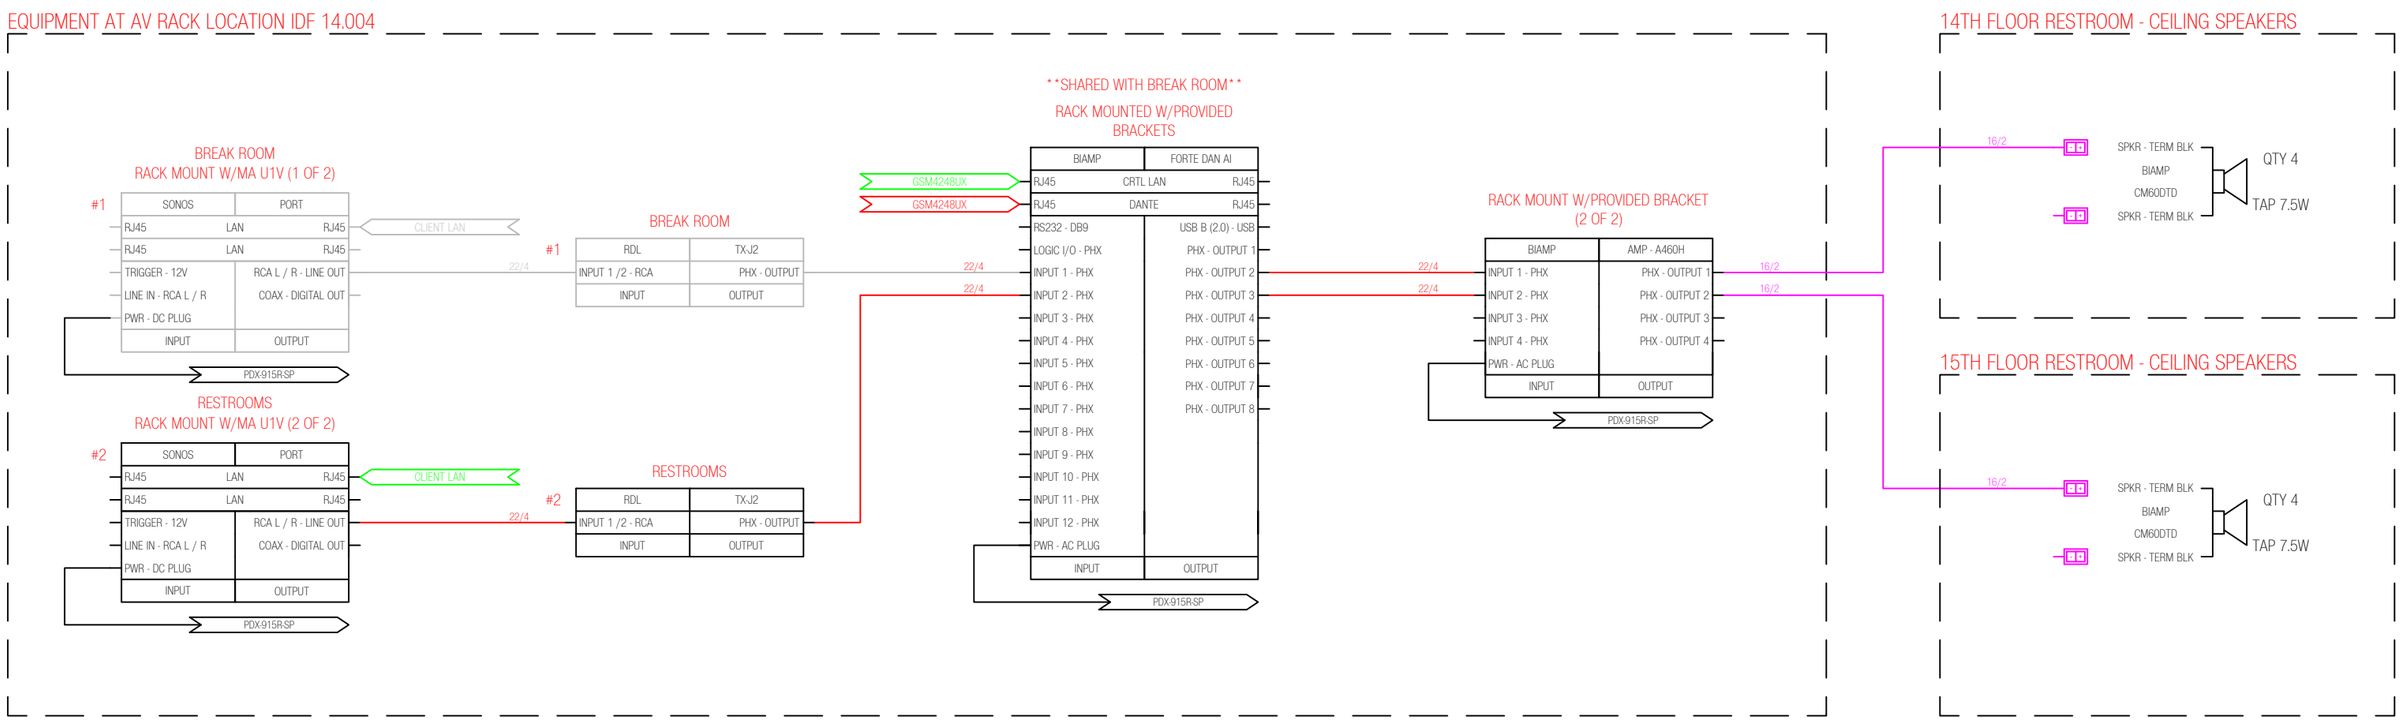

LEAD TECHNICIAN (PRINT): _____

NETWORK REQUIREMENTS			POWER REQUIREMENTS		
QTY	DEVICE	LOCATION	QTY	CIRCUIT/SIZE	LOCATION
-	SEE TA-724	RACK LOCATION	1	15A DUPLEX	RACK LOCATION
-	-	-	-	-	-
-	-	-	-	-	-
-	-	-	-	-	-
-	-	-	-	-	-
-	-	-	-	-	-
-	-	-	-	-	-
-	-	-	-	-	-
-	-	-	-	-	-
-	-	-	-	-	-

CLIENT NAME: LOCKTON DUNNING

REV:	DATE:	DRAWN BY:
0	03/05/2026	AFS
-	-	-

TAURUS technologies
1420 LAKESIDE PARKWAY, SUITE 100, FLOWER MOUND, TX 75028
WWW.TAURUSTECHINC.COM 1-888-410-5747

ROOM NAME: VICTORY COMMONS - 14TH & 15TH FLOOR - RESTROOMS

SITE ADDRESS: 2601 VICTORY AVE, DALLAS, TX 75219

PROJECT NO: JT022715, JT023560, JT023785, JT023822, JT023861 & JT023995

SHEET SIZE:	SCALE:	SHEET NO:
11 X 17	1 : 1	TA-729

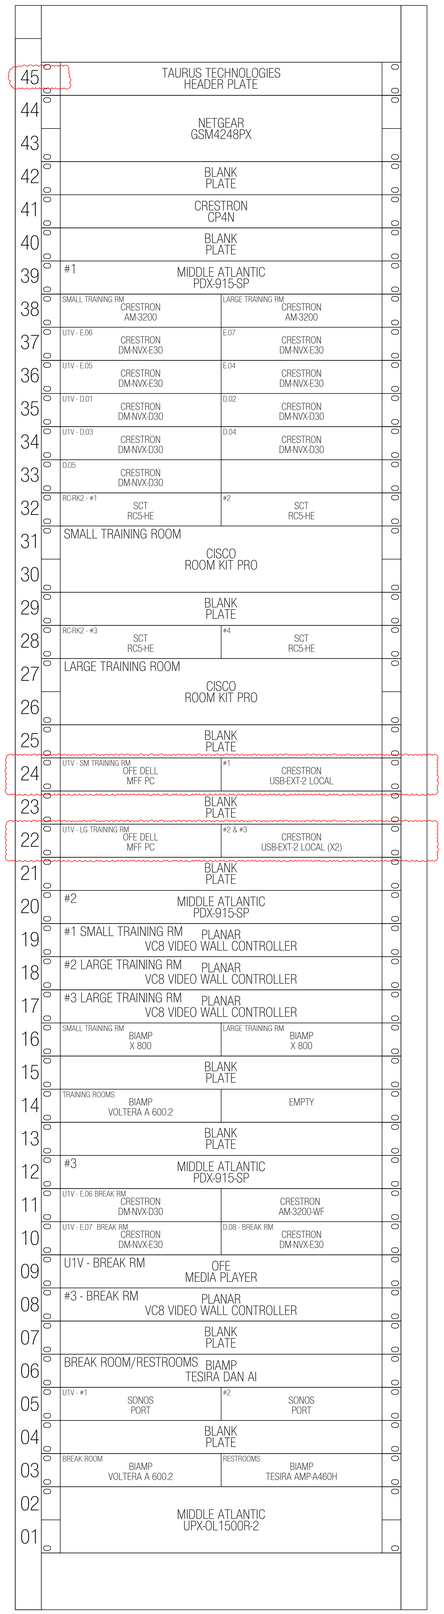

NETGEAR GSM4248PX	1706.071
CRESTRON CP4N W/CRESNET	136.48568
CRESTRON AM-3200	47.769988
CRESTRON DM-NVX-E30 E.03	51.18213
CRESTRON DM-NVX-E30 E.04	51.18213
CRESTRON DM-NVX-E30 E.05	51.18213
CRESTRON DM-NVX-E30 E.06	51.18213
CRESTRON DM-NVX-D30 D.01	54.594272
CRESTRON DM-NVX-D30 D.02	54.594272
CRESTRON DM-NVX-D30 D.03	54.594272
CRESTRON DM-NVX-D30 D.04	54.594272
SCT RC5-HE #1 W/CAM	129.661396
SCT RC5-HE #2 W/CAM	129.661396
CISCO ROOM KIP PRO #1	153.54639
PLANAR VC8-L-C5G VW CTRL #1	238.84994
OFE ROOM PC #1	443.57846
CRESTRON USB-EXT-2 LOCAL #1	81.891408
CRESTRON AM-3200	47.769988
CRESTRON DM-NVX-D30 E.05	54.594272
SCT RC5-HE #3 W/CAM	129.661396
SCT RC5-HE #4 W/CAM	129.661396
CISCO ROOM KIP PRO #2	153.54639
PLANAR VC8-L-C5G VW CTRL #2	238.84994
PLANAR VC8-L-C5G VW CTRL #3	238.84994
BIAMP X800	511.8213
BIAMP VOLTERA A 600.2	682.4284
OFE ROOM PC #2	443.57846
CRESTRON USB-EXT-2 LOCAL #2	81.891408
CRESTRON AM-3200	47.769988
CRESTRON DM-NVX-E30 E.05	51.18213
CRESTRON DM-NVX-E30 E.06	51.18213
CRESTRON DM-NVX-D30 D.04	54.594272
OFE MEDIA PLAYER	85.30355
PLANAR VC8-L-C5G VW CTRL #4	238.84994
BIAMP FORTE DAN CI	119.42497
SONOS PORT #1	12.2837112
SONOS PORT #2	12.2837112
BIAMP VOLTERA A 600.2	682.4284
BIAMP TEIRA AMP-A460H	204.72852
MIDLE ATLANTIC UPX-OL 1500R-1	528.88201
BTU TOTAL	8292.19

AV RACK ROOM 14.004 - EQUIPMENT RACK

LEAD TECHNICIAN (PRINT):

CLIENT NAME: LOCKTON DUNNING	ROOM NAME: VICTORY COMMONS - 14TH FLR. - RACK ELEVATION		
REV: 0	DATE: 03/26/2026	DRAWN BY: AFS	SITE ADDRESS: 2601 VICTORY AVE, DALLAS, TX 75219
			PROJECT NO: JT022715, JT023560, JT023785, JT023822, JT023861 & JT023995
TAURUS technologies 1420 LAKESIDE PARKWAY, SUITE 100, FLOWER MOUND, TX 75028 WWW.TAURUSTECHINC.COM T-888-410-5747	SHEET SIZE: 36 X 48	SCALE: 1:10	SHEET NO: TA-730